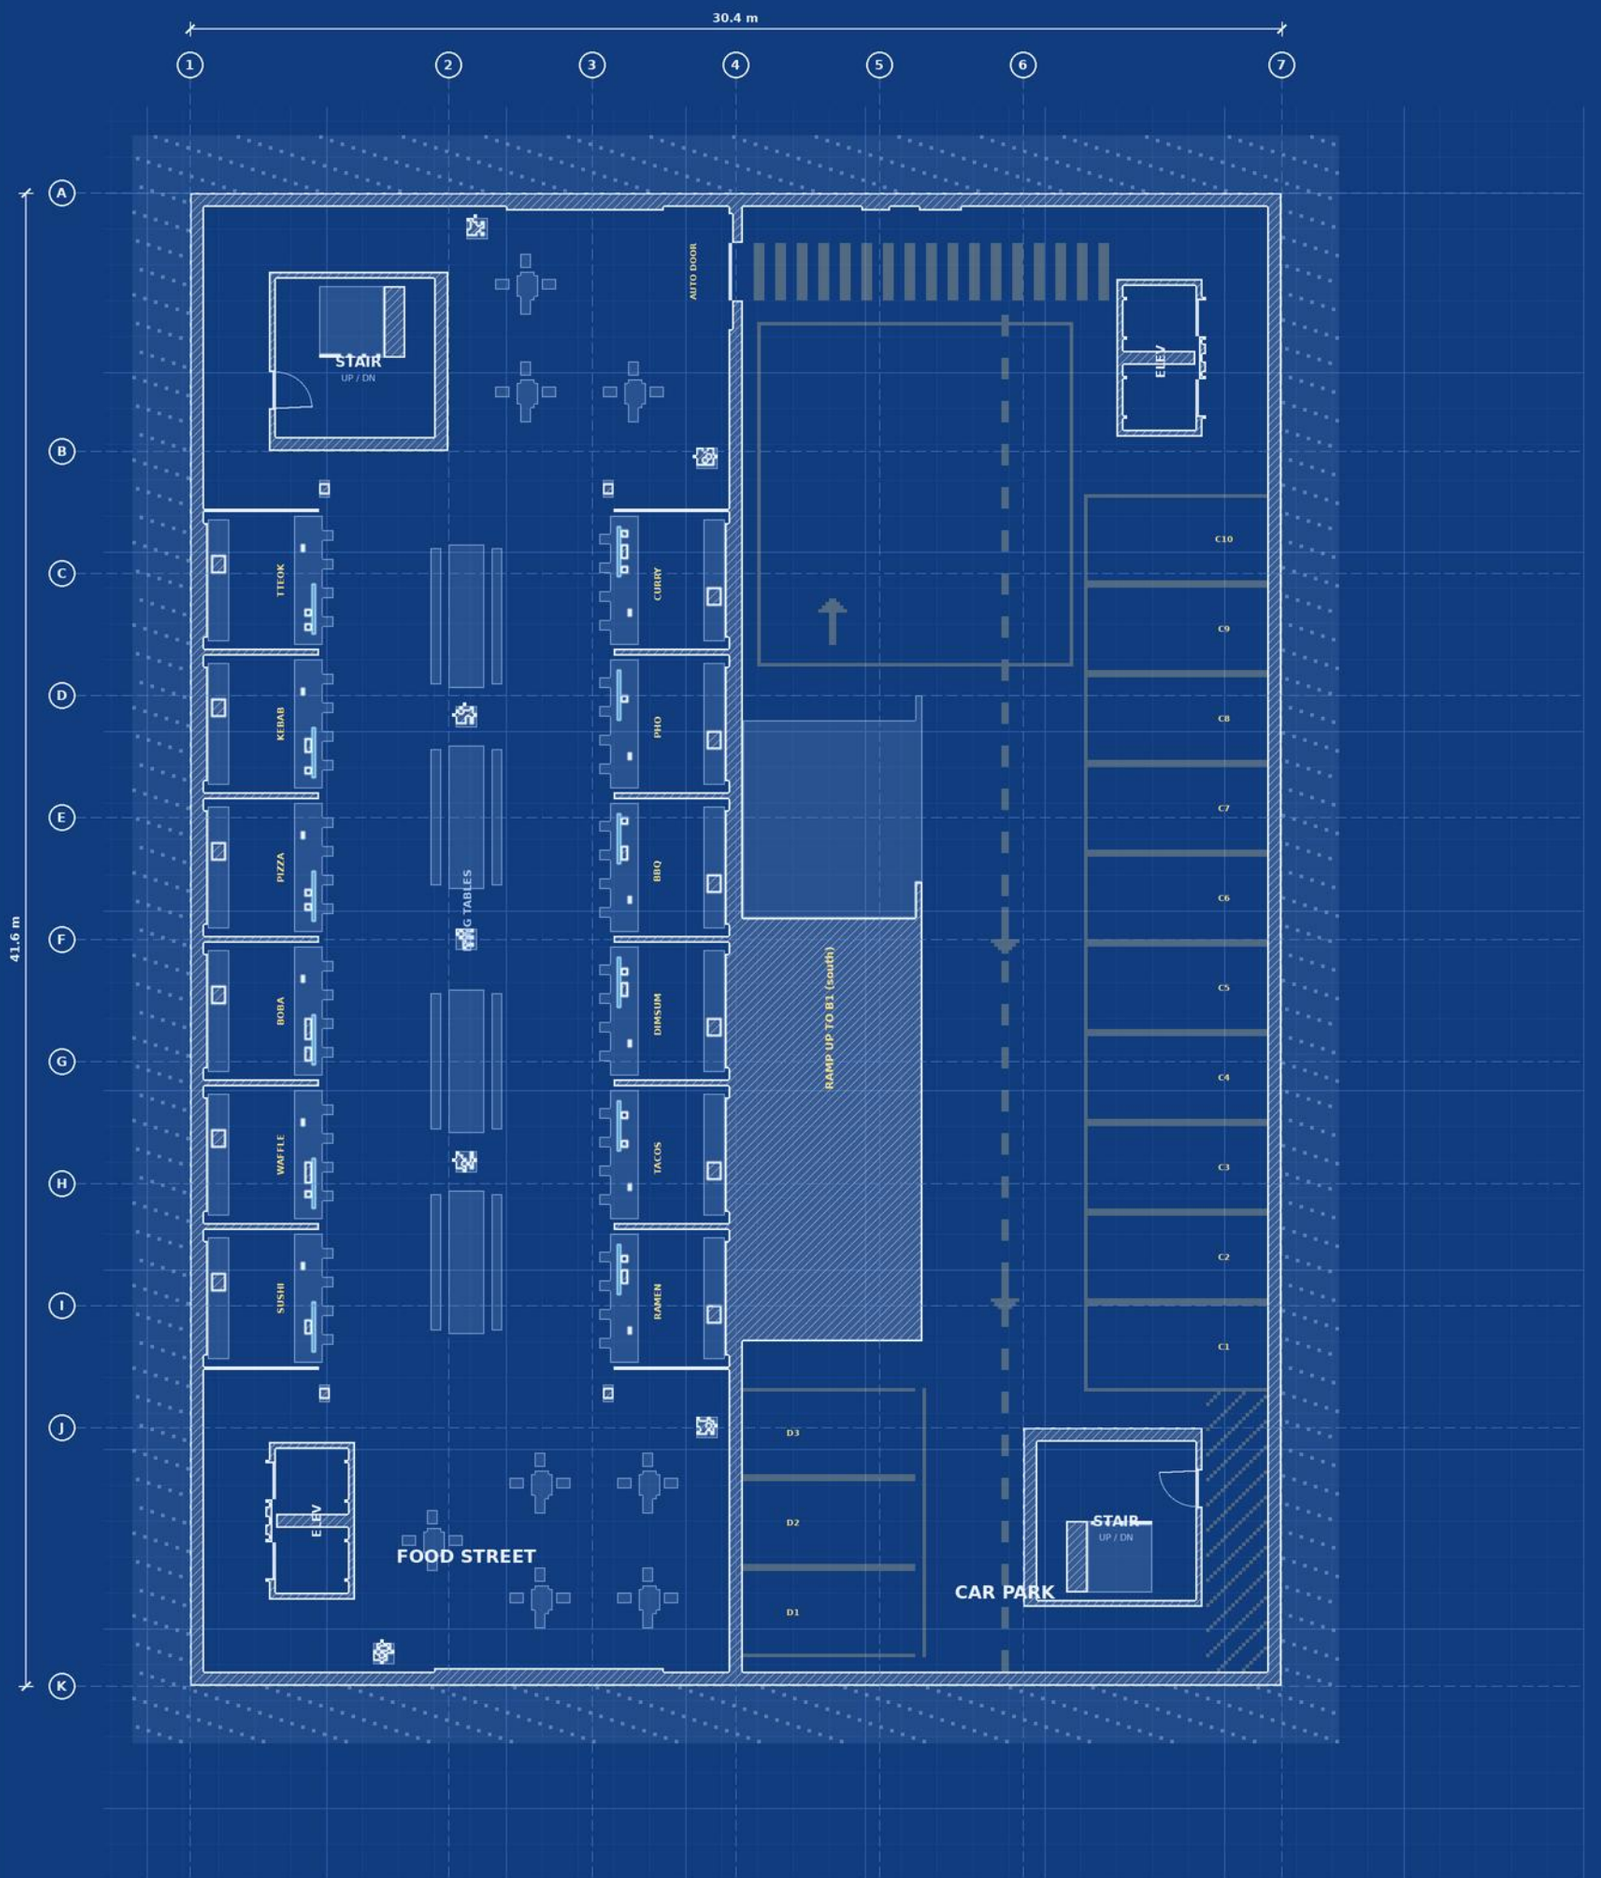


LIMINAL ATRIUM HOTEL

LEVEL B2 - FOOD STREET & CAR PARK

Floor -7.2 m. Cut at +1.2 m above floor.

Food street: 12 stalls (6 a side) with neon signs and awnings, long tables, neon gates, cafe courts.
Parking: 13 bays (C, D), right under the B1 car park: ramp from B1.

N

SCALE 1:100 (1 voxel = 10 cm)

0 2.5 5 7.5 10 m


SHEET

A-099

DATE 2026-11-14

DRAWN Claude | SOURCE tools/build_map.py

Teardown map mod - Liminal Atrium

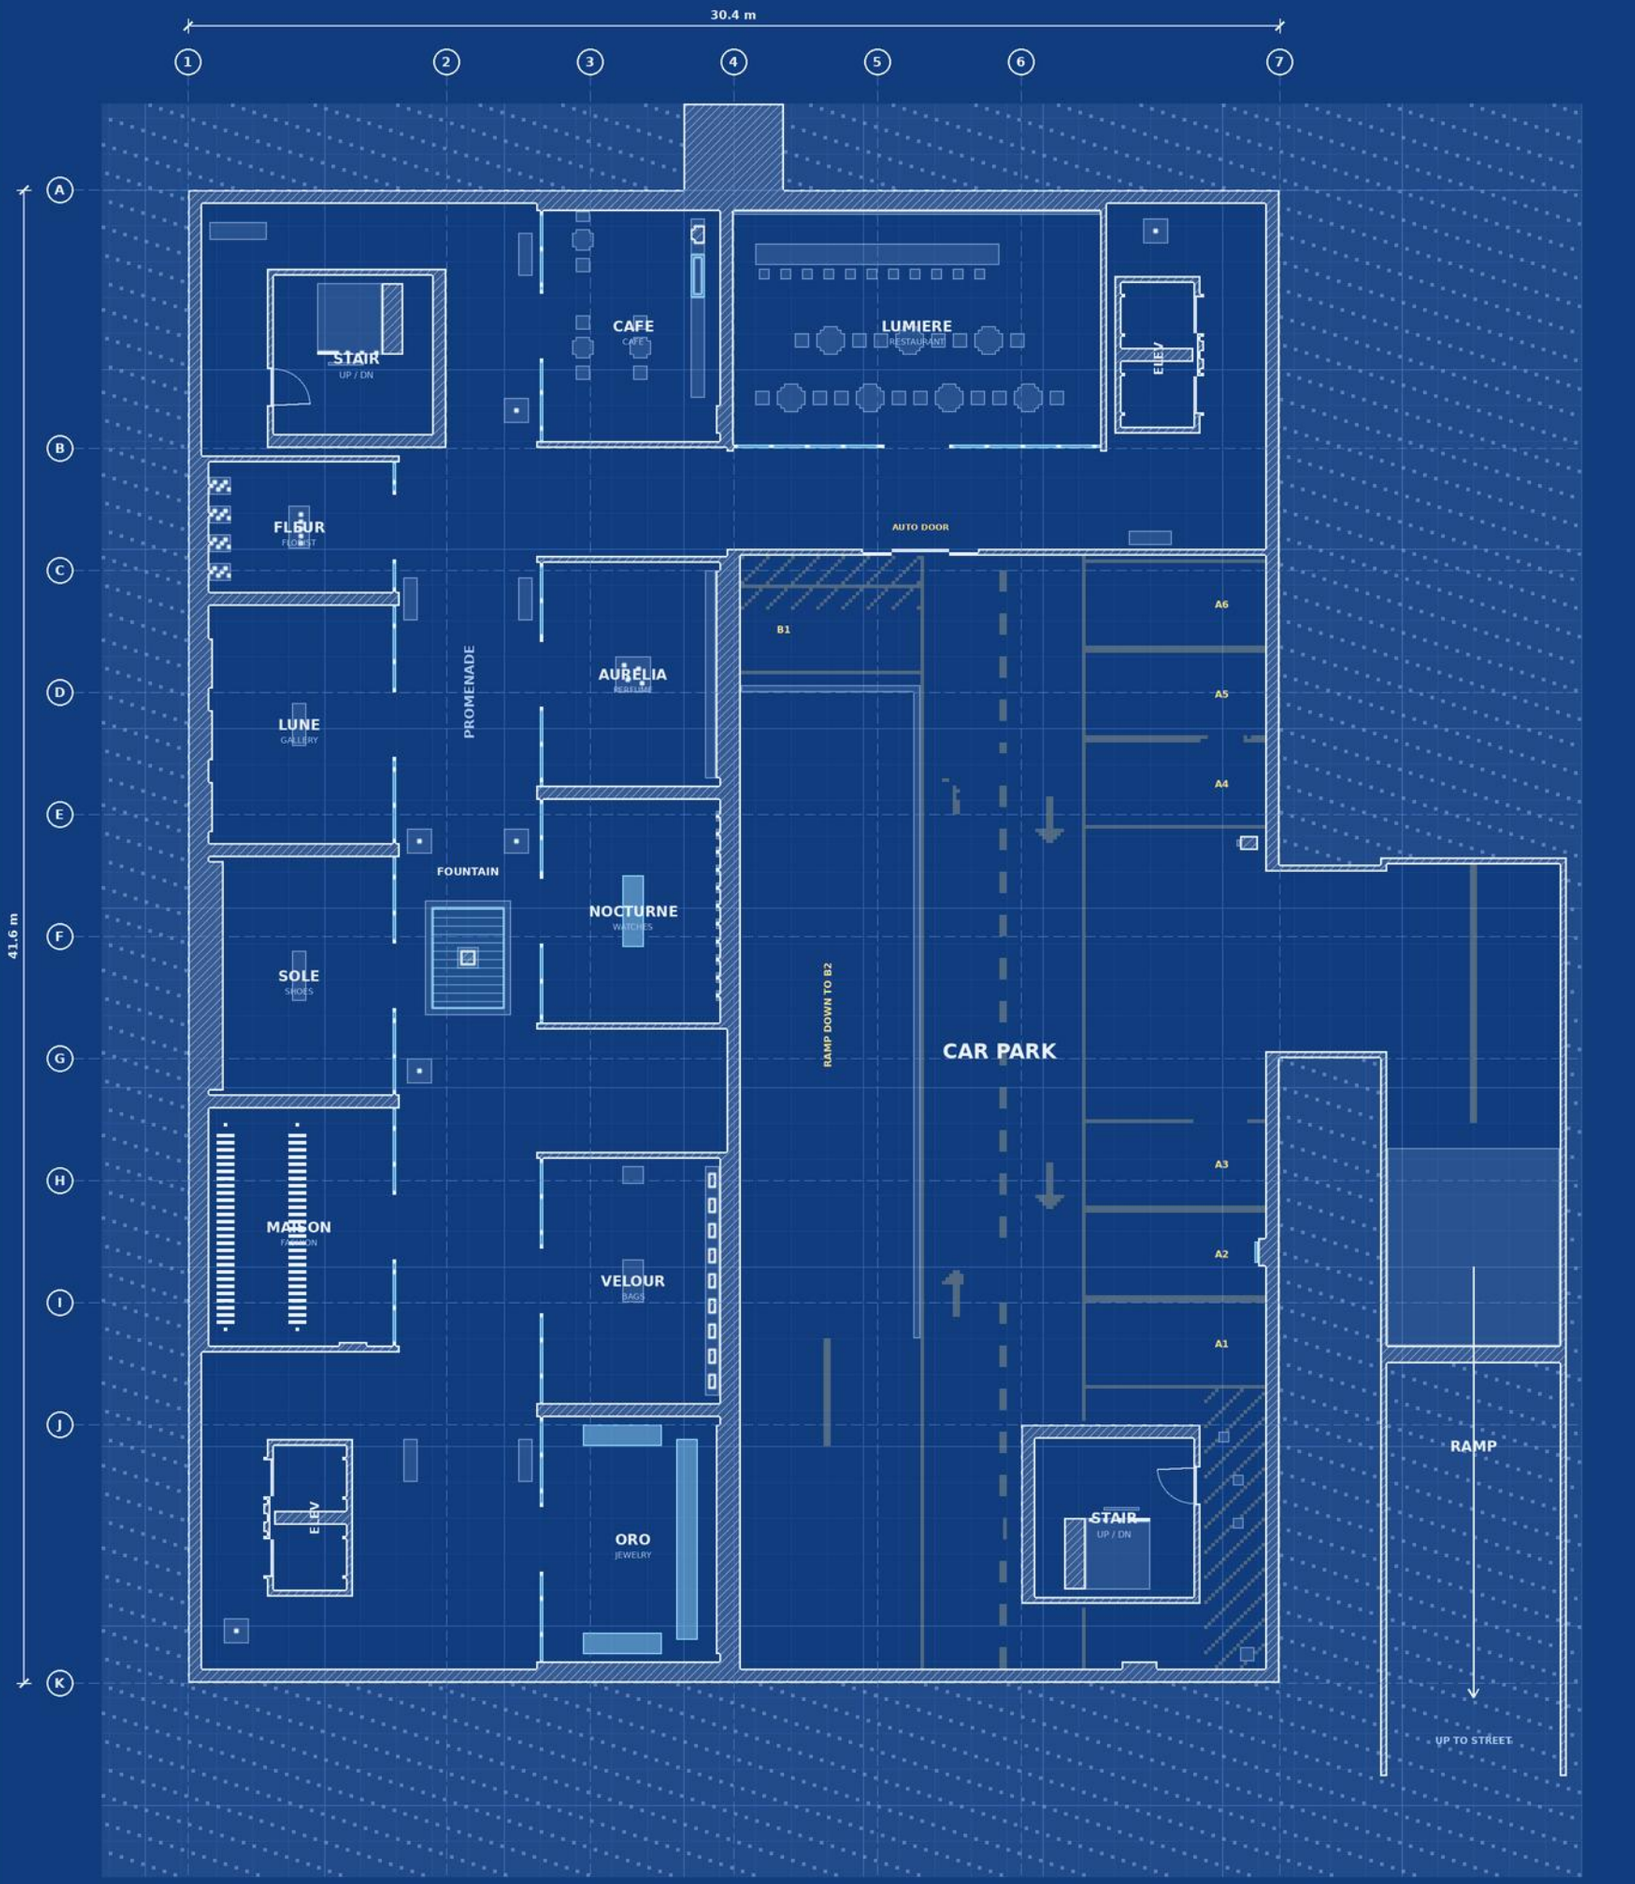

LIMINAL ATRIUM HOTEL

LEVEL B1 - CAR PARK & LUXURY ARCADE

Floor -3.6 m. Cut at +1.2 m above floor.

Parking: 7 bays 2.5 x 5.0 m (A1-A6, B1), 90-degree, reverse in. Ramp down to B2 from the south end, along the arcade wall. Columns 0.6 x 0.6 m on the aisle edge. Hatched: no parking.

N

SCALE 1:100 (1 voxel = 10 cm)

0 2.5 5 7.5 10 m

SHEET

A-100

DATE 2026-11-14

DRAWN Claude | SOURCE tools/build_map.py

Teardown map mod - Liminal Atrium

30.4 m

1 2 3 4 5 6 7

A B C D E F G H I J K

41.6 m

POOL HALL

SPA

POOL

GLASS CONNECTOR

CORRIDOR

STAIR
UP / DN

BOILER
STAFF ONLY

LAUNDRY
STAFF ONLY

KITCHEN
STAFF ONLY

ELEC

ELEV

109 GUEST ROOM

110 GUEST ROOM

111 GUEST ROOM

112 GUEST ROOM

113 GUEST ROOM

114 GUEST ROOM

115 GUEST ROOM

116 GUEST ROOM

CORRIDOR

ATRIUM
6 storeys, open to the roof lantern

CORRIDOR

108 GUEST ROOM

107 GUEST ROOM

106 GUEST ROOM

105 GUEST ROOM

104 GUEST ROOM

103 GUEST ROOM

102 GUEST ROOM

101 GUEST ROOM

ELEV

ELEC

117 GUEST ROOM

LOBBY

120 GUEST ROOM

STAIR
UP / DN

CORRIDOR

MAIN ENTRANCE

LIMINAL ATRIUM HOTEL

LEVEL 1 - LOBBY, GUEST ROOMS & POOLROOMS

Floor +/-0.0 (pool hall deck +2.0 m). Cut at +1.2 m above floor.

Room numbers are drawing references (floor x 100 + room).
Pool hall deck is 2.0 m above the ground floor; shown cut at +1.2 m from the deck.


N

SCALE 1:100 (1 voxel = 10 cm)

0 2.5 5 7.5 10 m

SHEET
A-101

DATE 2026-11-14
DRAWN Claude | SOURCE tools/build_map.py
Teardown map mod - Liminal Atrium

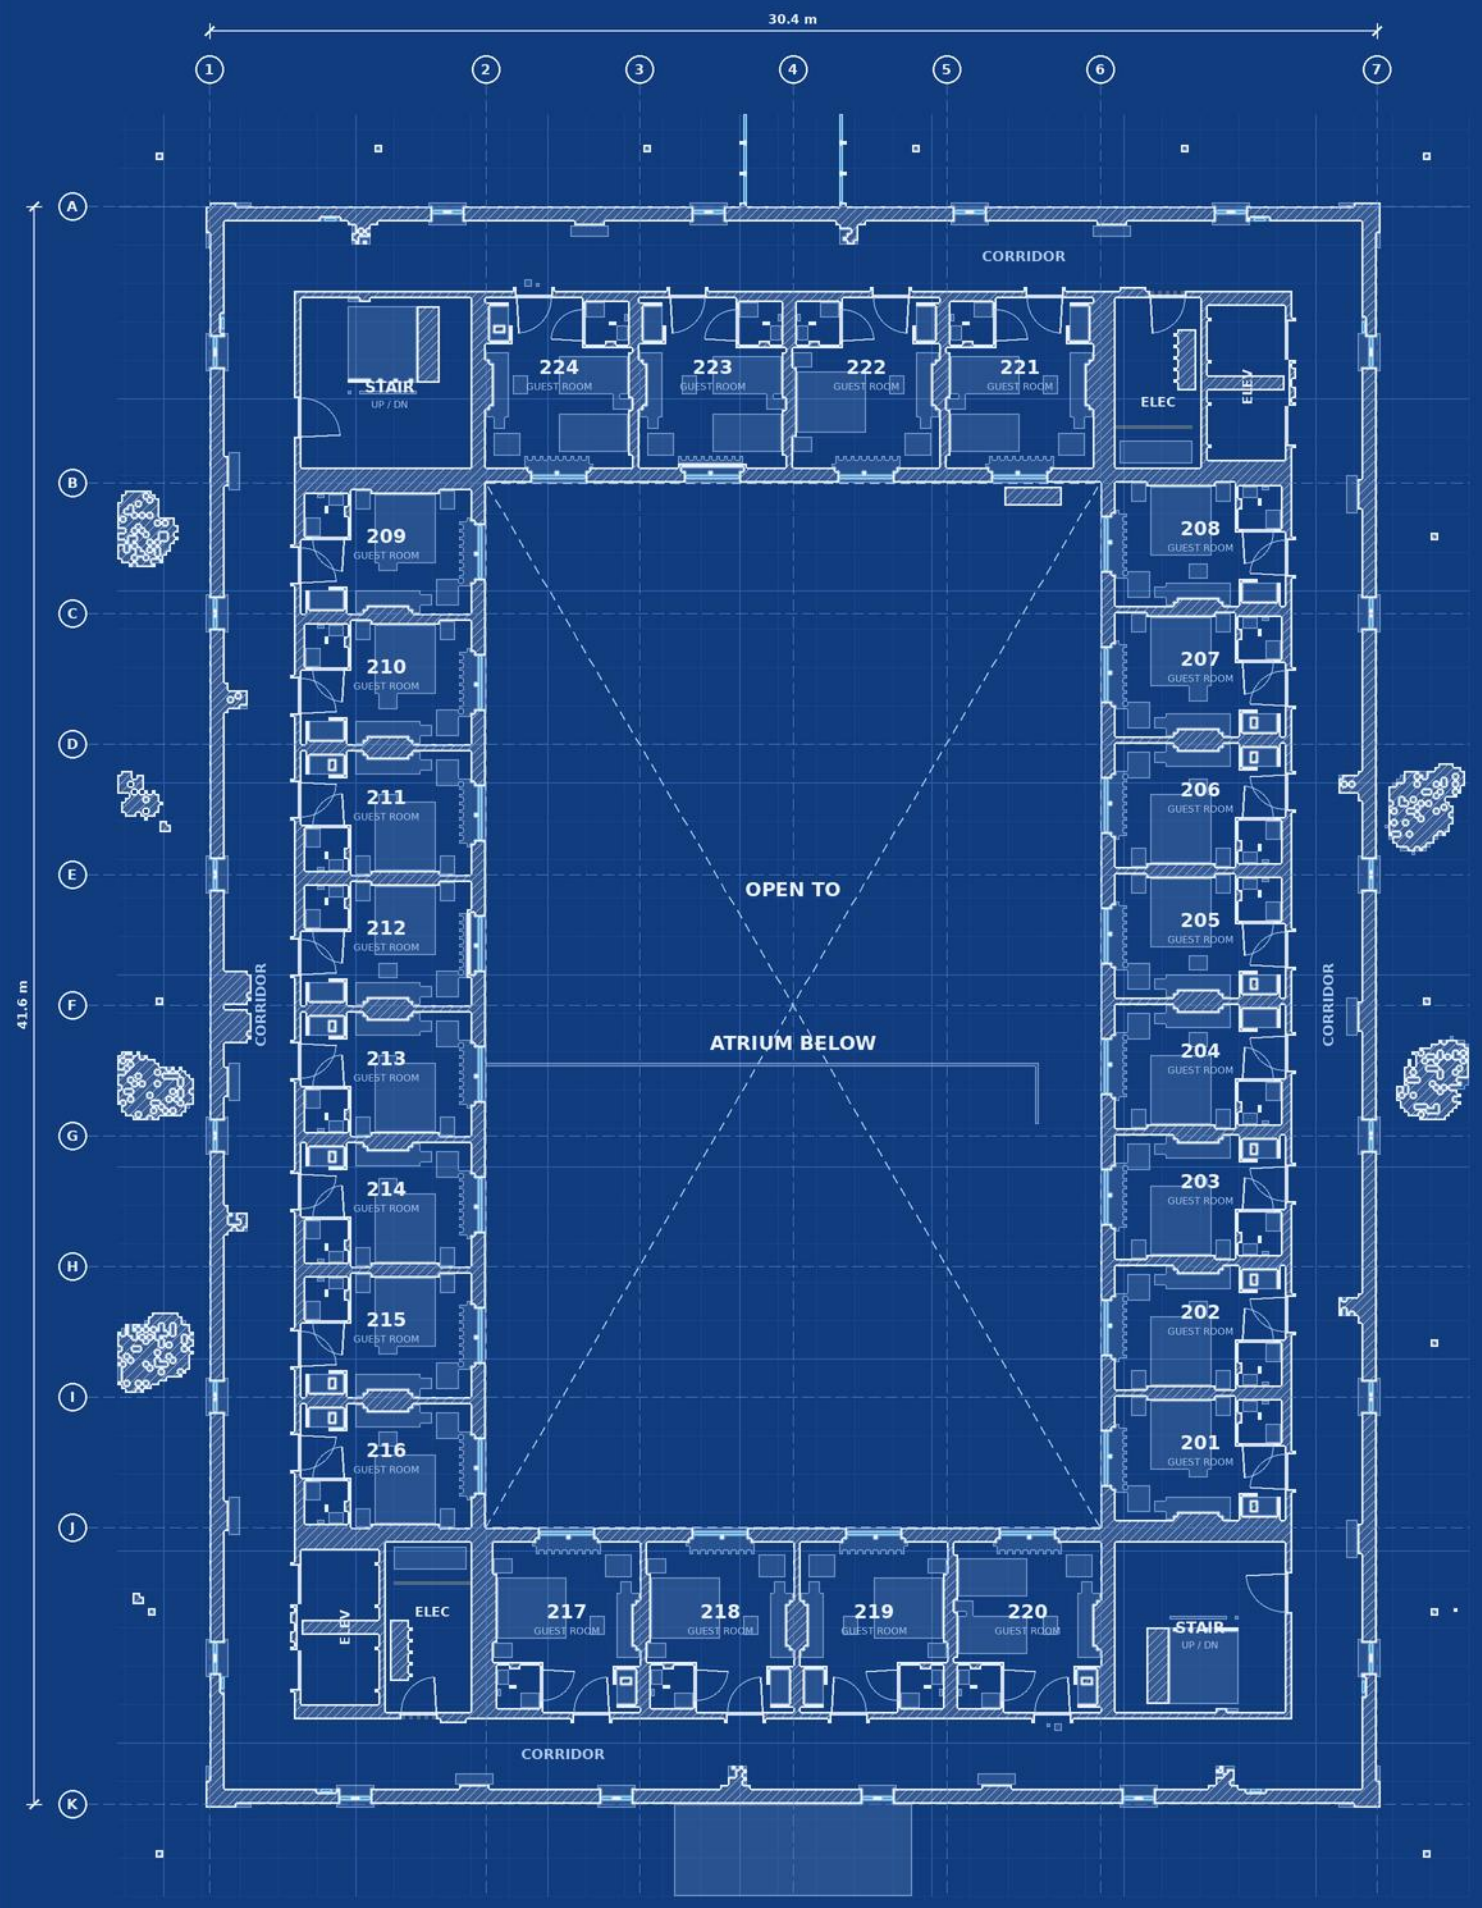

LIMINAL ATRIUM HOTEL

LEVEL 2 - GUEST FLOOR

Floor +3.0 m. Cut at +1.2 m above floor. Corridor theme: zigzag.

Room numbers are drawing references (floor x 100 + room).
Electrical rooms by the elevators feed this floor (E: switch, destroyed: blackout).

N

SCALE 1:100 (1 voxel = 10 cm)

0 2.5 5 7.5 10 m


SHEET

A-102

DATE 2026-11-14

DRAWN Claude | SOURCE tools/build_map.py

Teardown map mod - Liminal Atrium

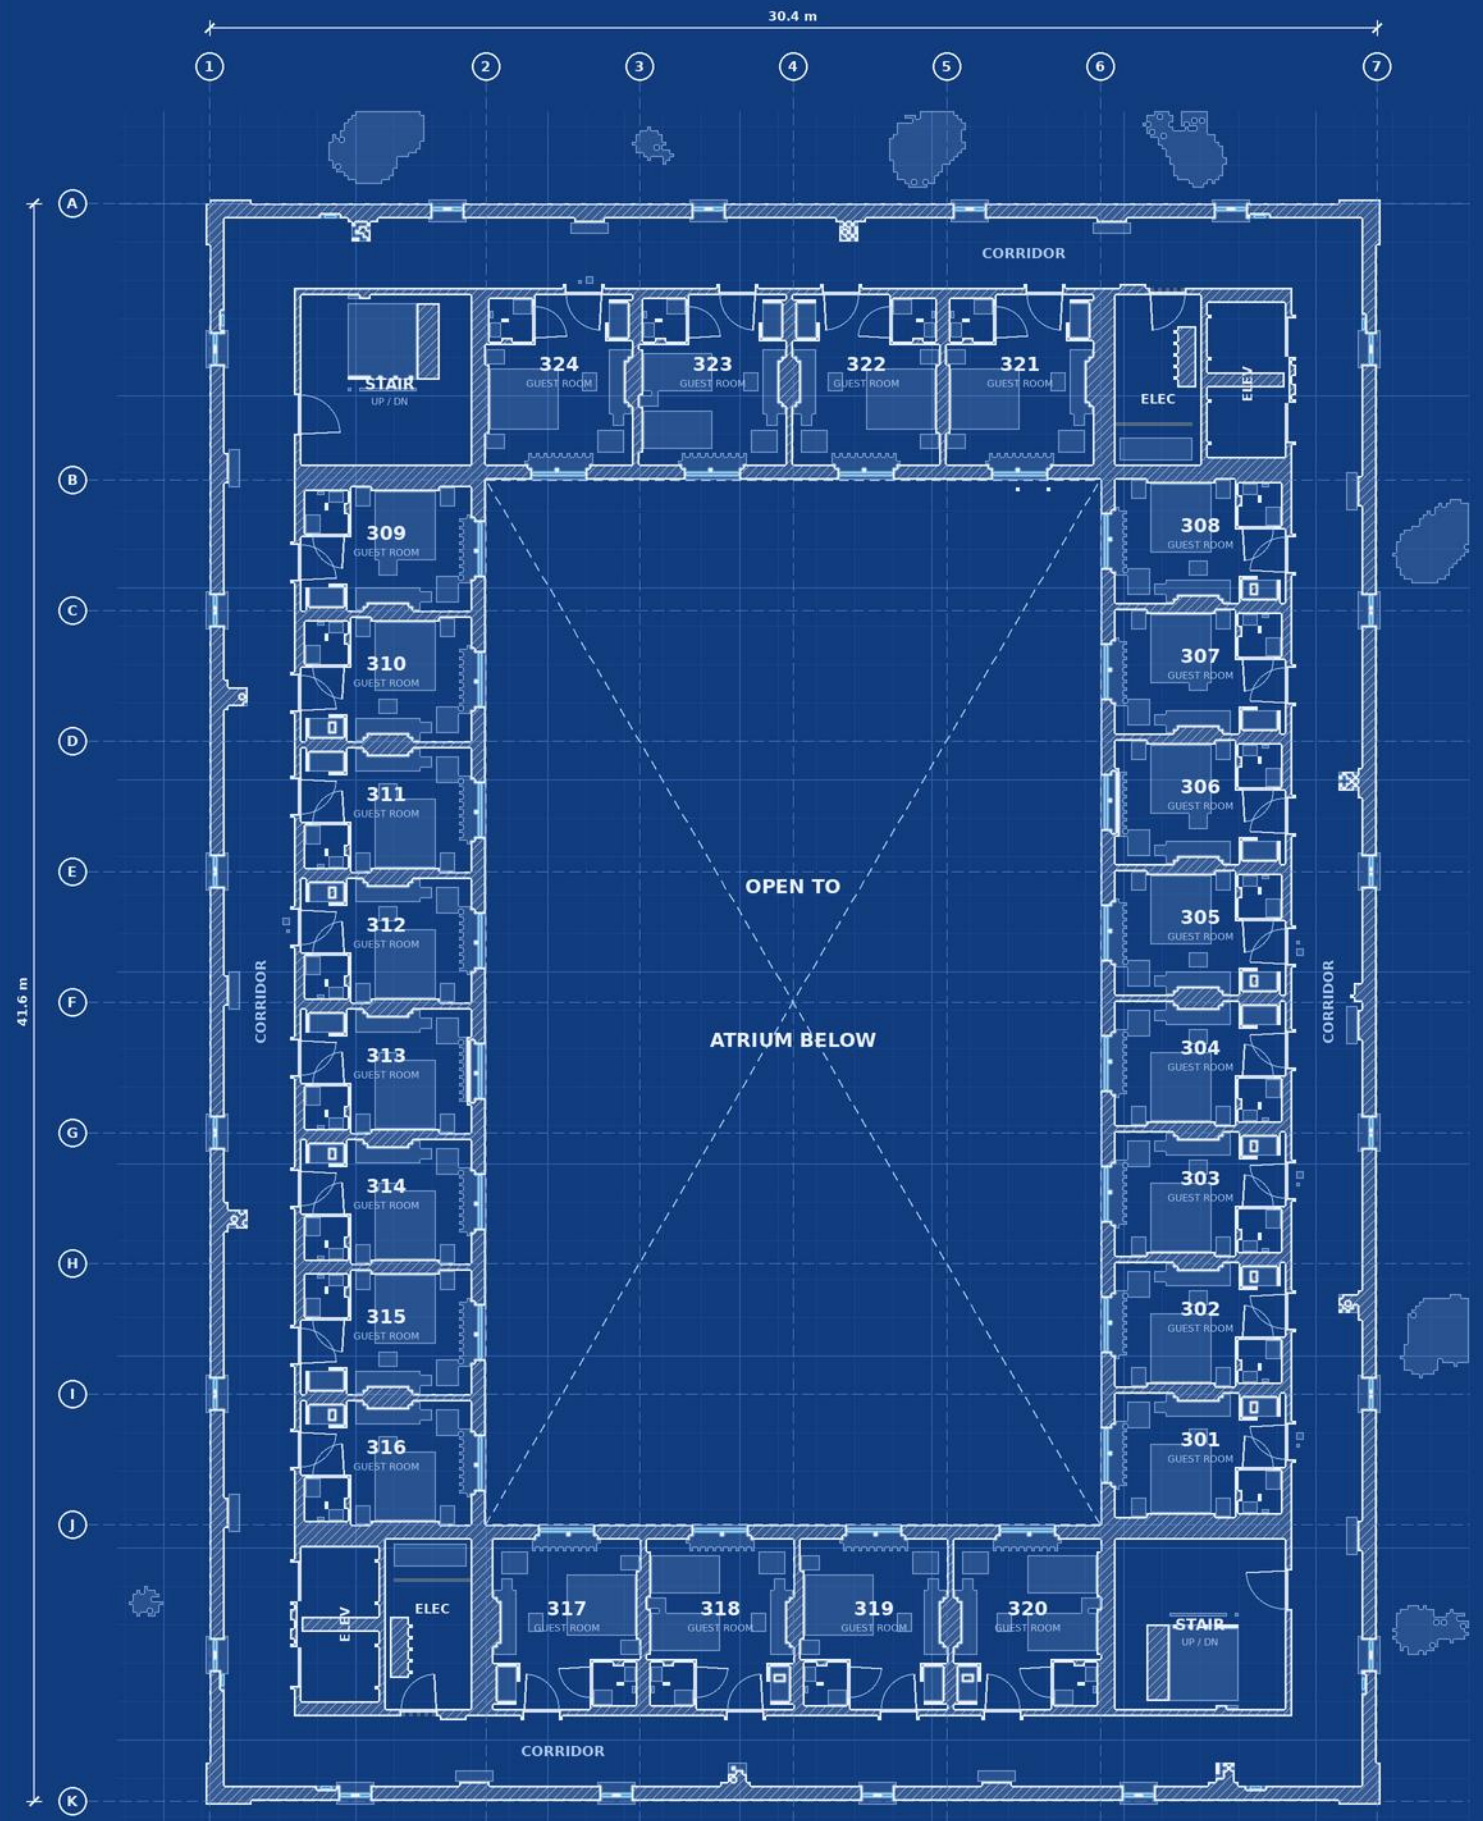

LIMINAL ATRIUM HOTEL

LEVEL 3 - GUEST FLOOR

Floor +6.0 m. Cut at +1.2 m above floor. Corridor theme: diamond.

Room numbers are drawing references (floor x 100 + room).
Electrical rooms by the elevators feed this floor (E: switch, destroyed: blackout).

N

SCALE 1:100 (1 voxel = 10 cm)

0 2.5 5 7.5 10 m


SHEET

A-103

DATE 2026-11-14

DRAWN Claude | SOURCE tools/build_map.py

Teardown map mod - Liminal Atrium

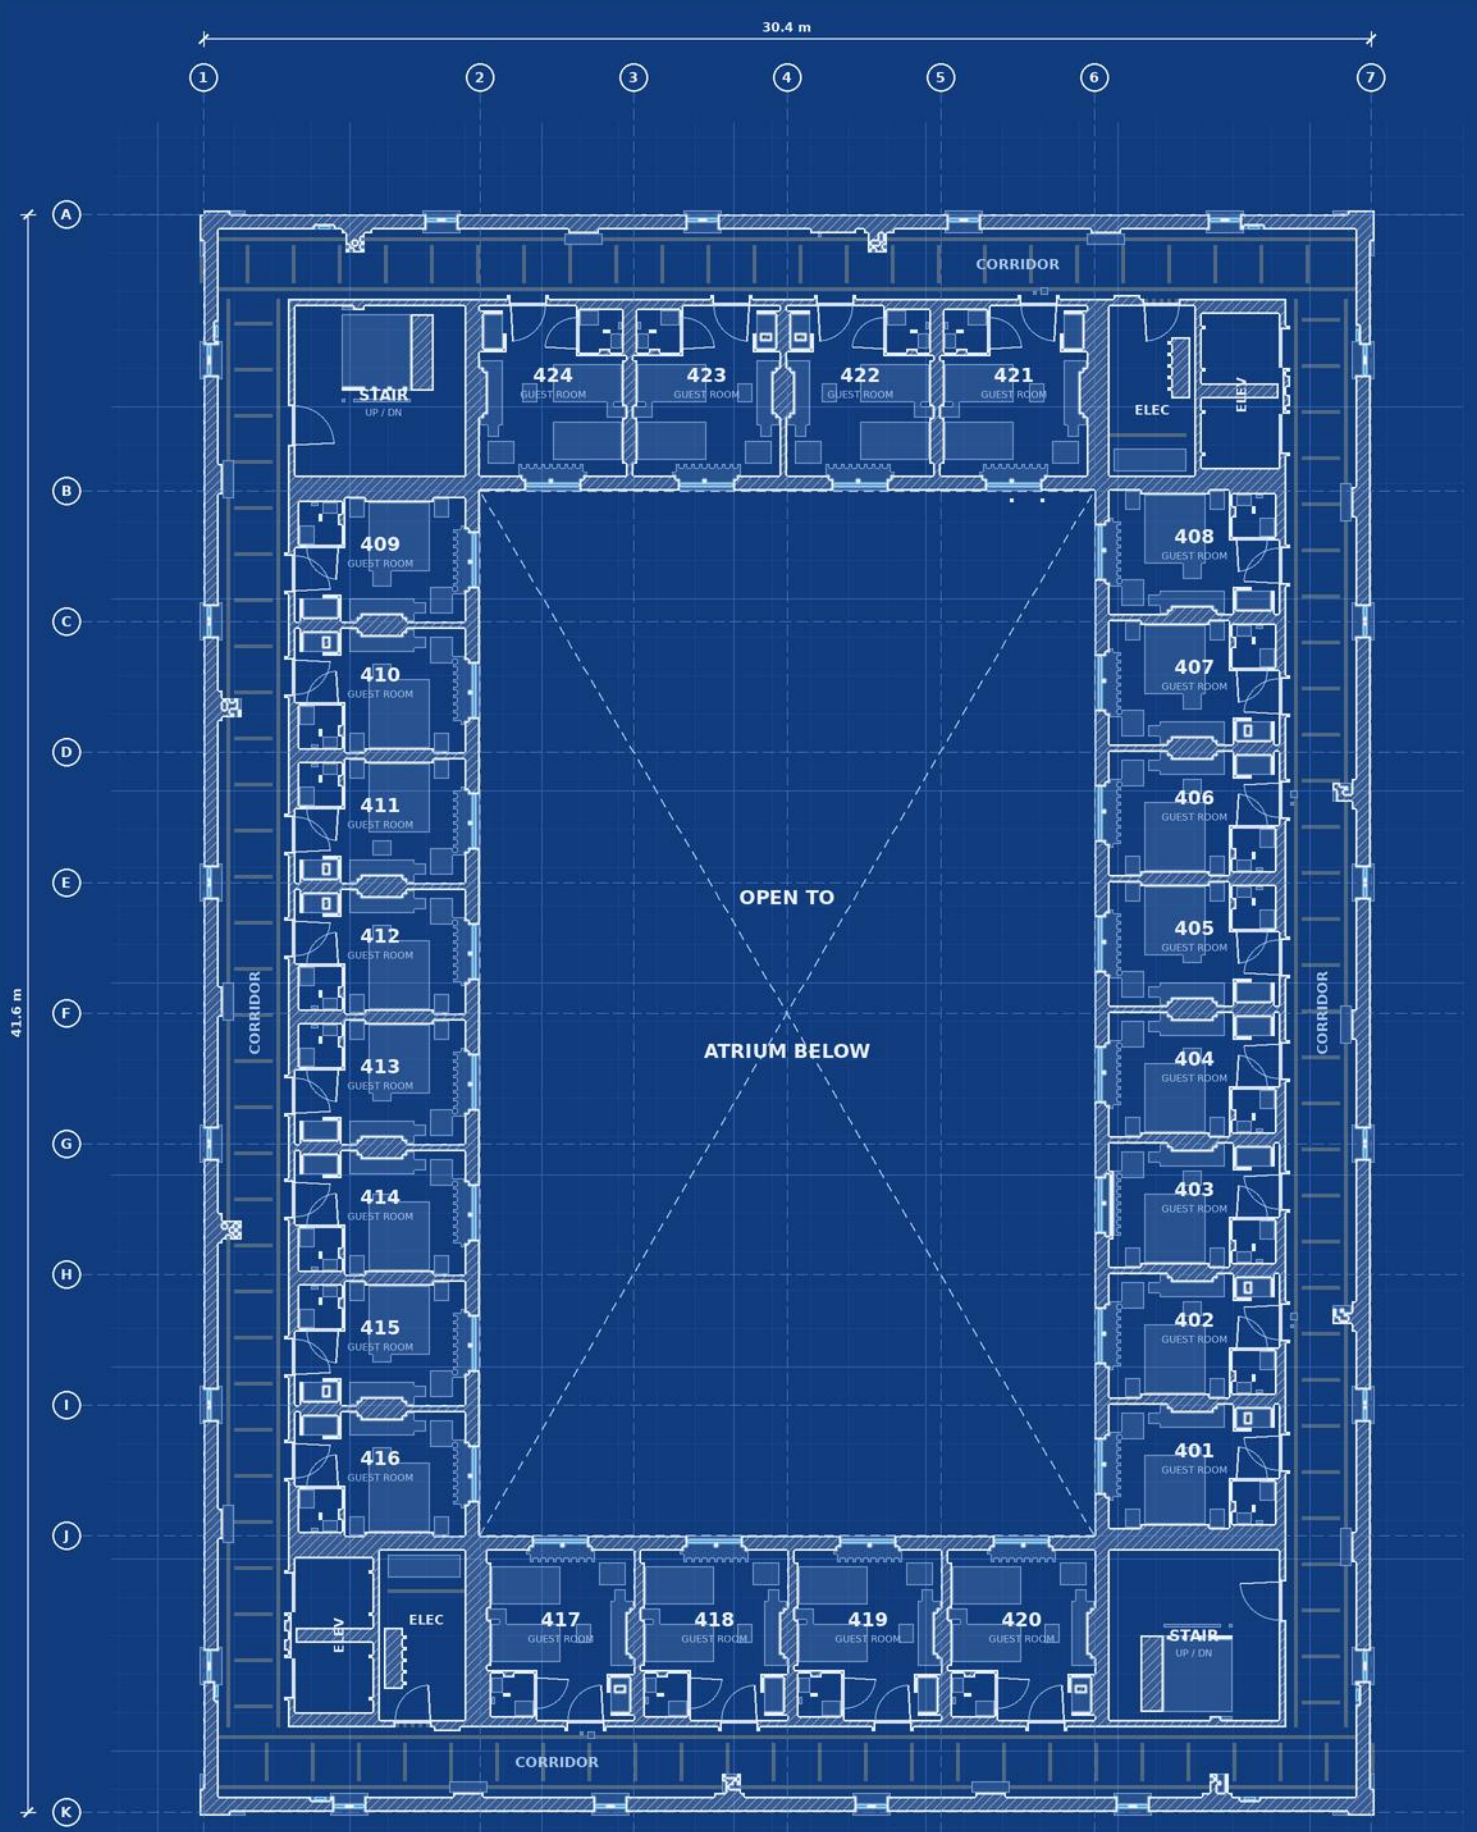

LIMINAL ATRIUM HOTEL

LEVEL 4 - GUEST FLOOR

Floor +9.0 m. Cut at +1.2 m above floor. Corridor theme: stripes.

Room numbers are drawing references (floor x 100 + room).
Electrical rooms by the elevators feed this floor (E: switch, destroyed: blackout).

N

SCALE 1:100 (1 voxel = 10 cm)

0 2.5 5 7.5 10 m


SHEET

A-104

DATE 2026-11-14

DRAWN Claude | SOURCE tools/build_map.py

Teardown map mod - Liminal Atrium

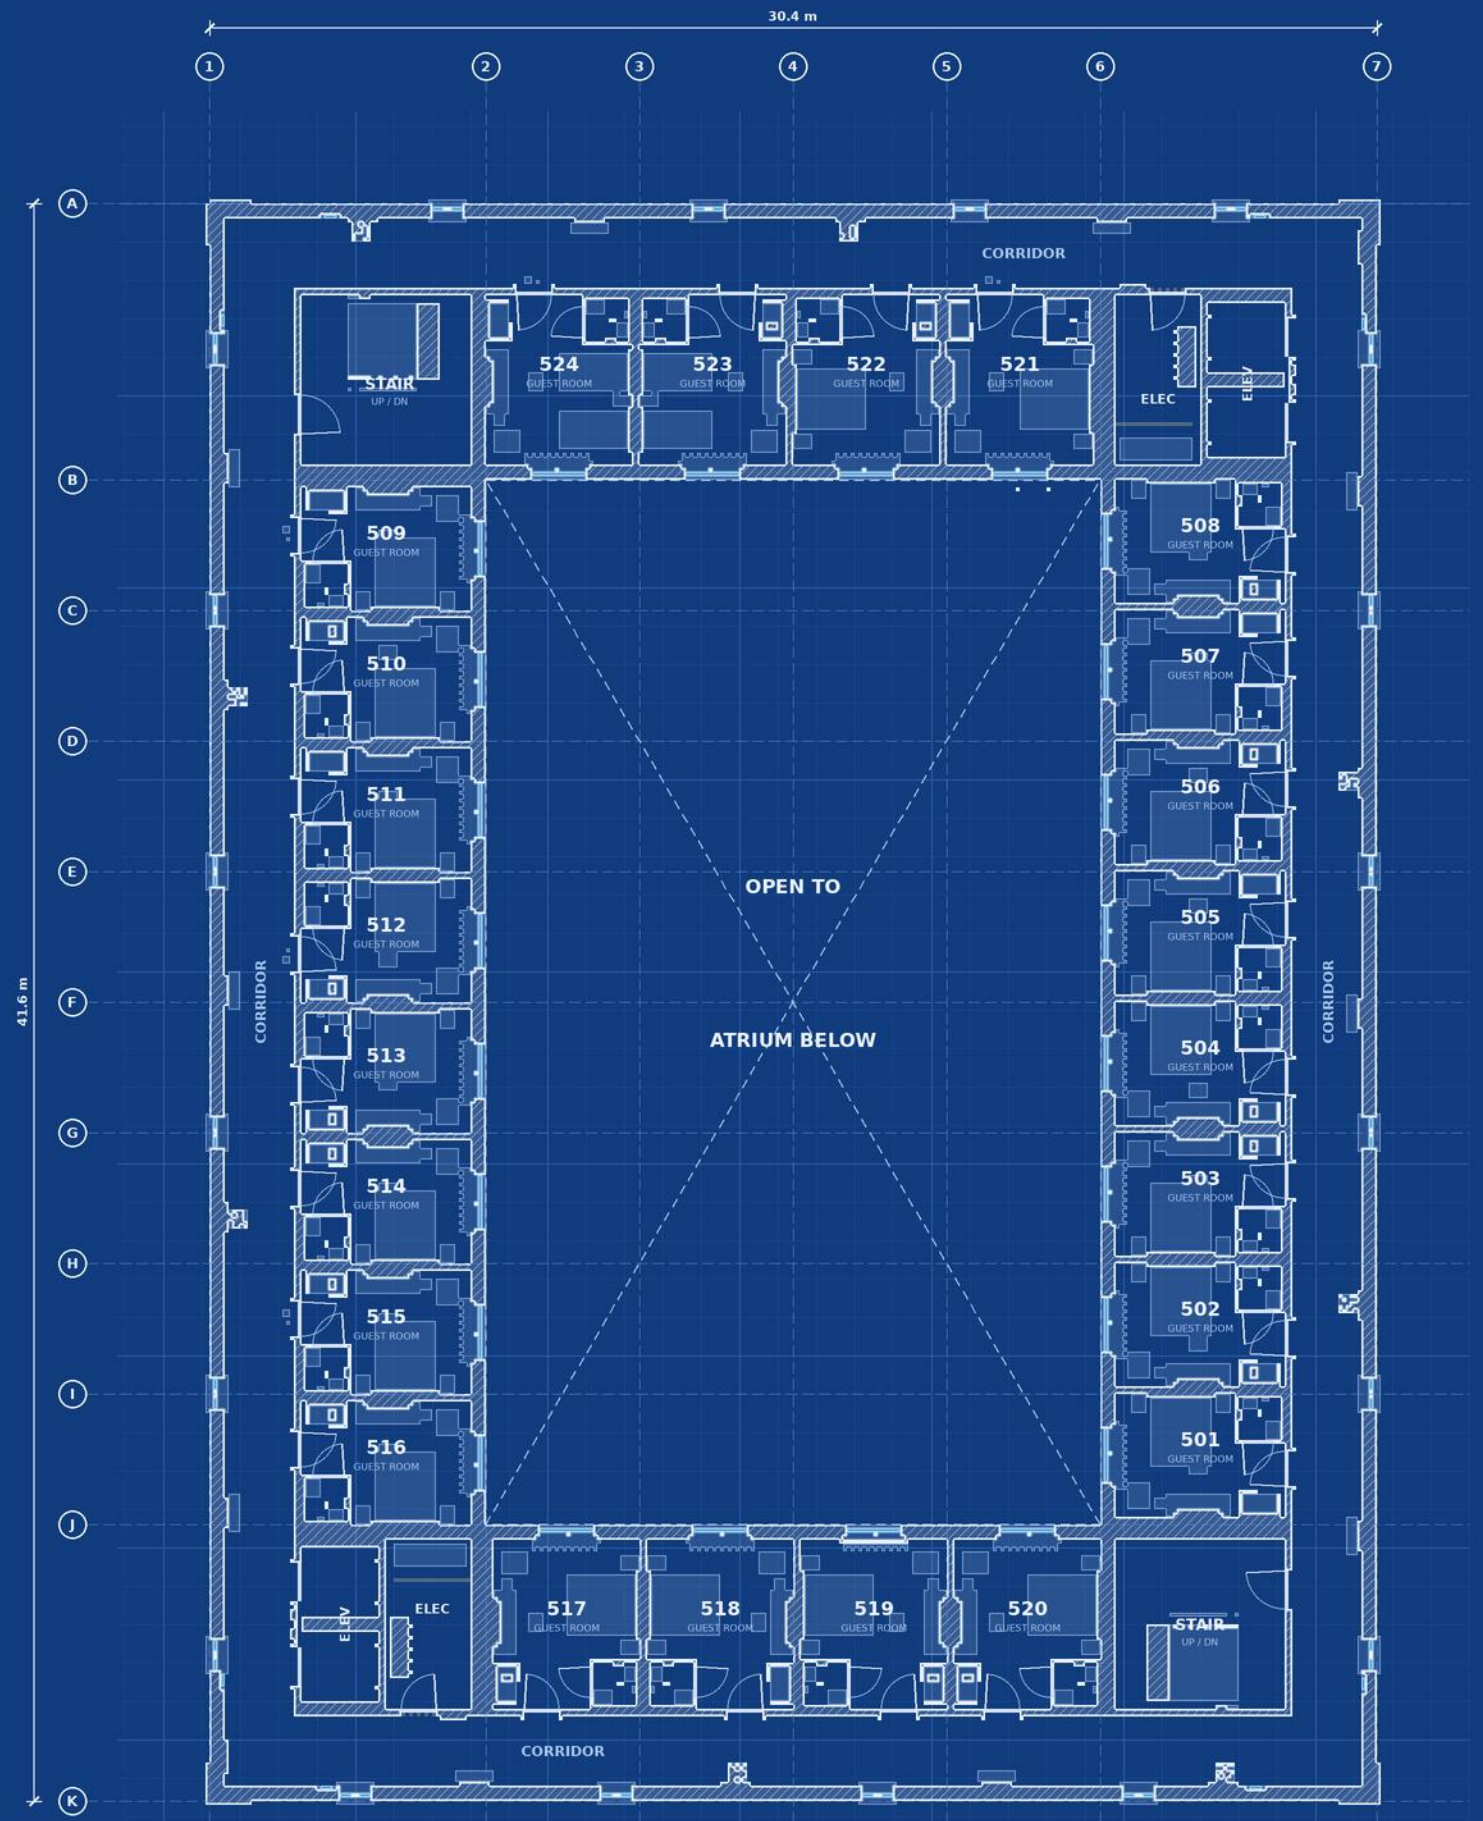

LIMINAL ATRIUM HOTEL

LEVEL 5 - GUEST FLOOR

Floor +12.0 m. Cut at +1.2 m above floor. Corridor theme: dots.

Room numbers are drawing references (floor x 100 + room).
Electrical rooms by the elevators feed this floor (E: switch, destroyed: blackout).

N

SCALE 1:100 (1 voxel = 10 cm)

0 2.5 5 7.5 10 m


SHEET

A-105

DATE 2026-11-14

DRAWN Claude | SOURCE tools/build_map.py

Teardown map mod - Liminal Atrium

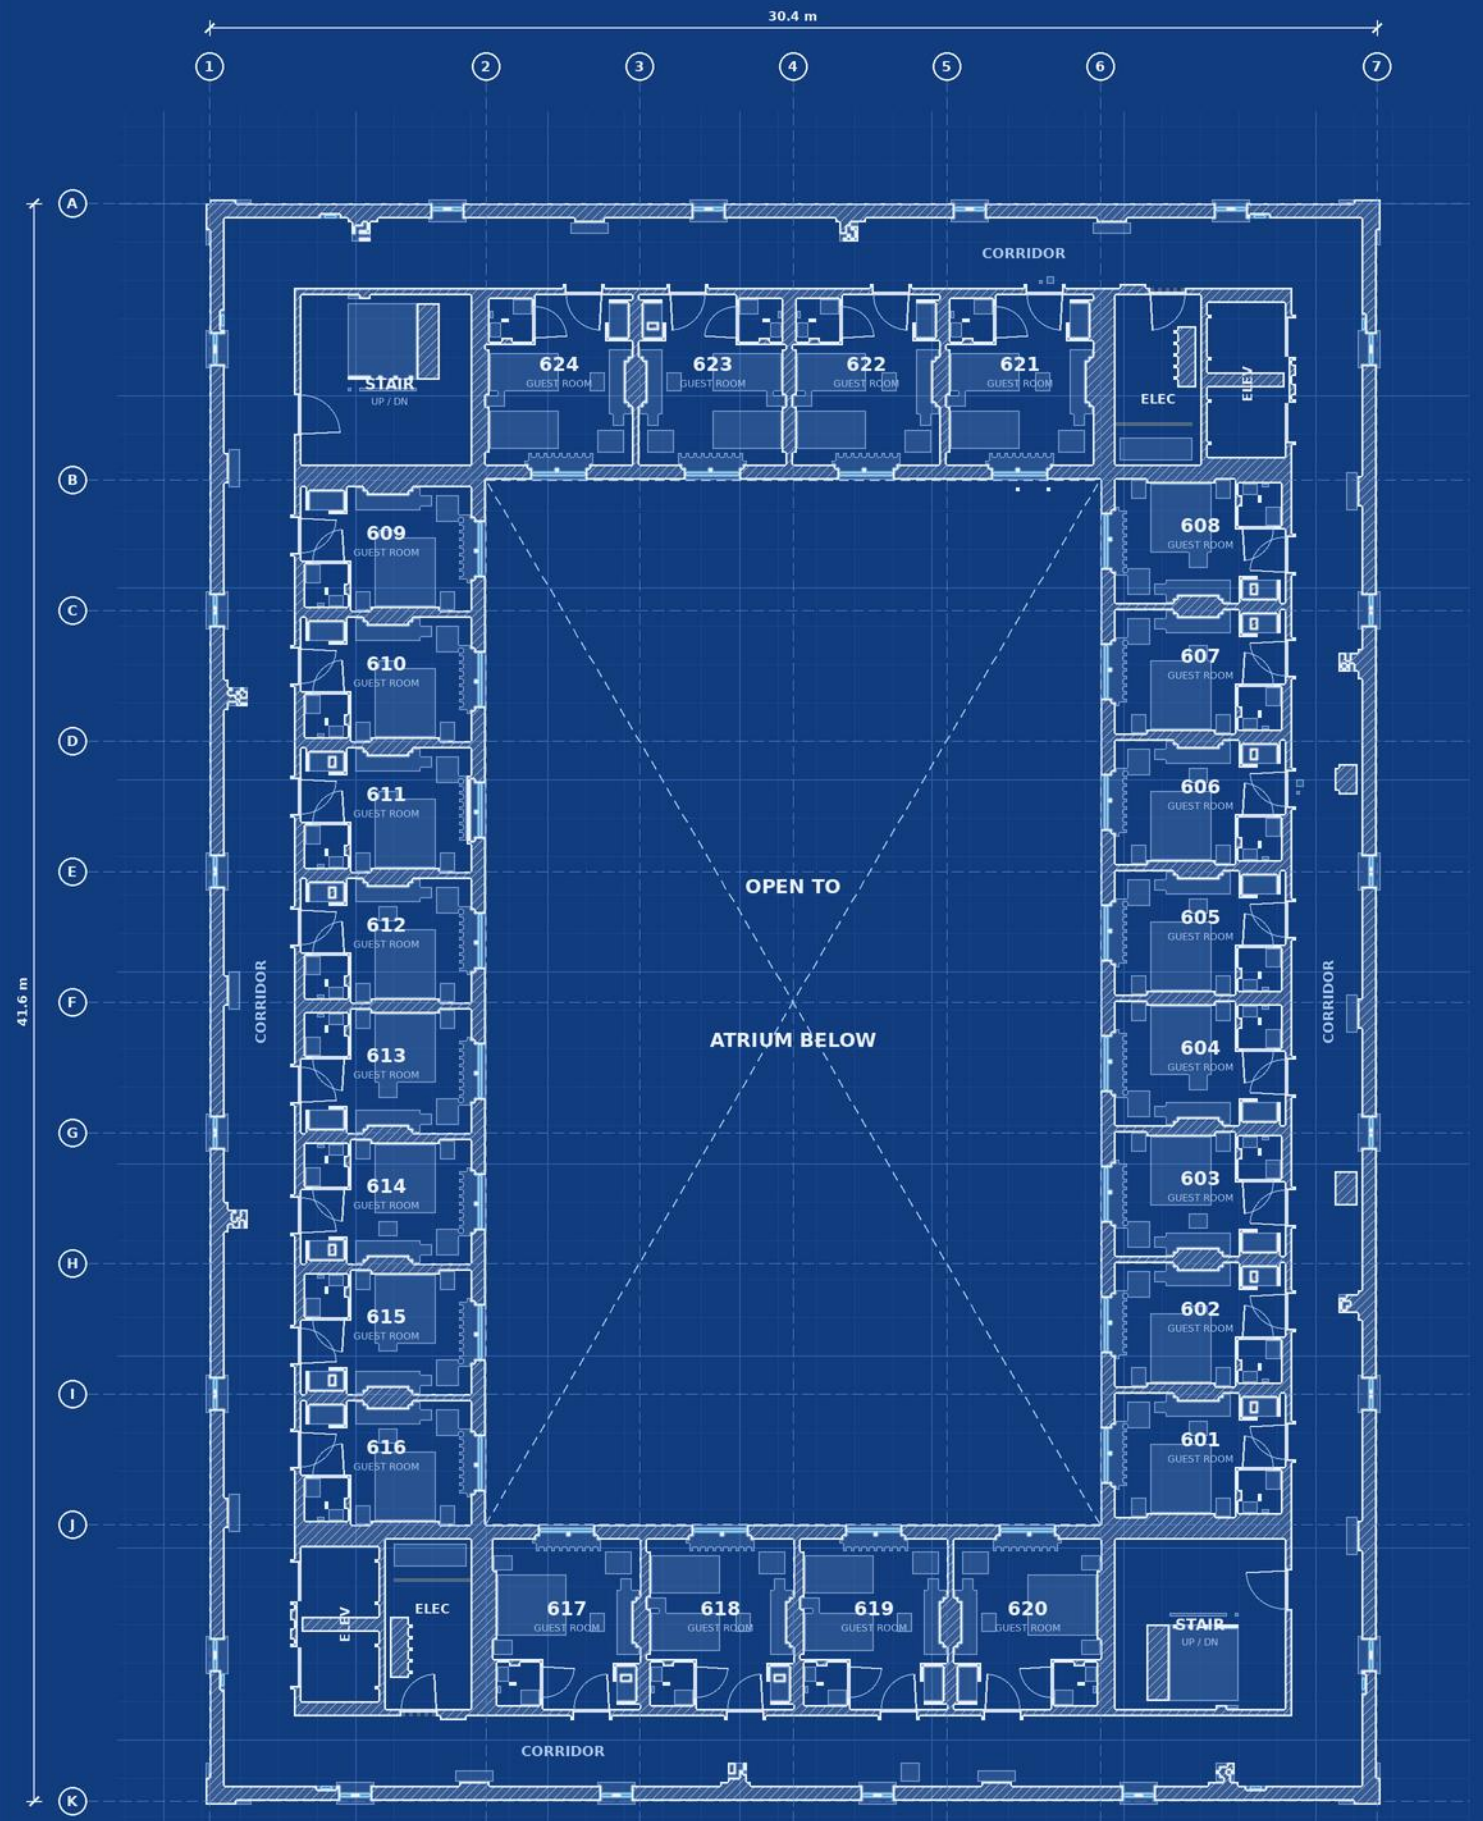

LIMINAL ATRIUM HOTEL

LEVEL 6 - GUEST FLOOR

Floor +15.0 m. Cut at +1.2 m above floor. Corridor theme: plain.

Room numbers are drawing references (floor x 100 + room).
Electrical rooms by the elevators feed this floor (E: switch, destroyed: blackout).

N

SCALE 1:100 (1 voxel = 10 cm)

0 2.5 5 7.5 10 m


SHEET

A-106

DATE 2026-11-14

DRAWN Claude | SOURCE tools/build_map.py

Teardown map mod - Liminal Atrium

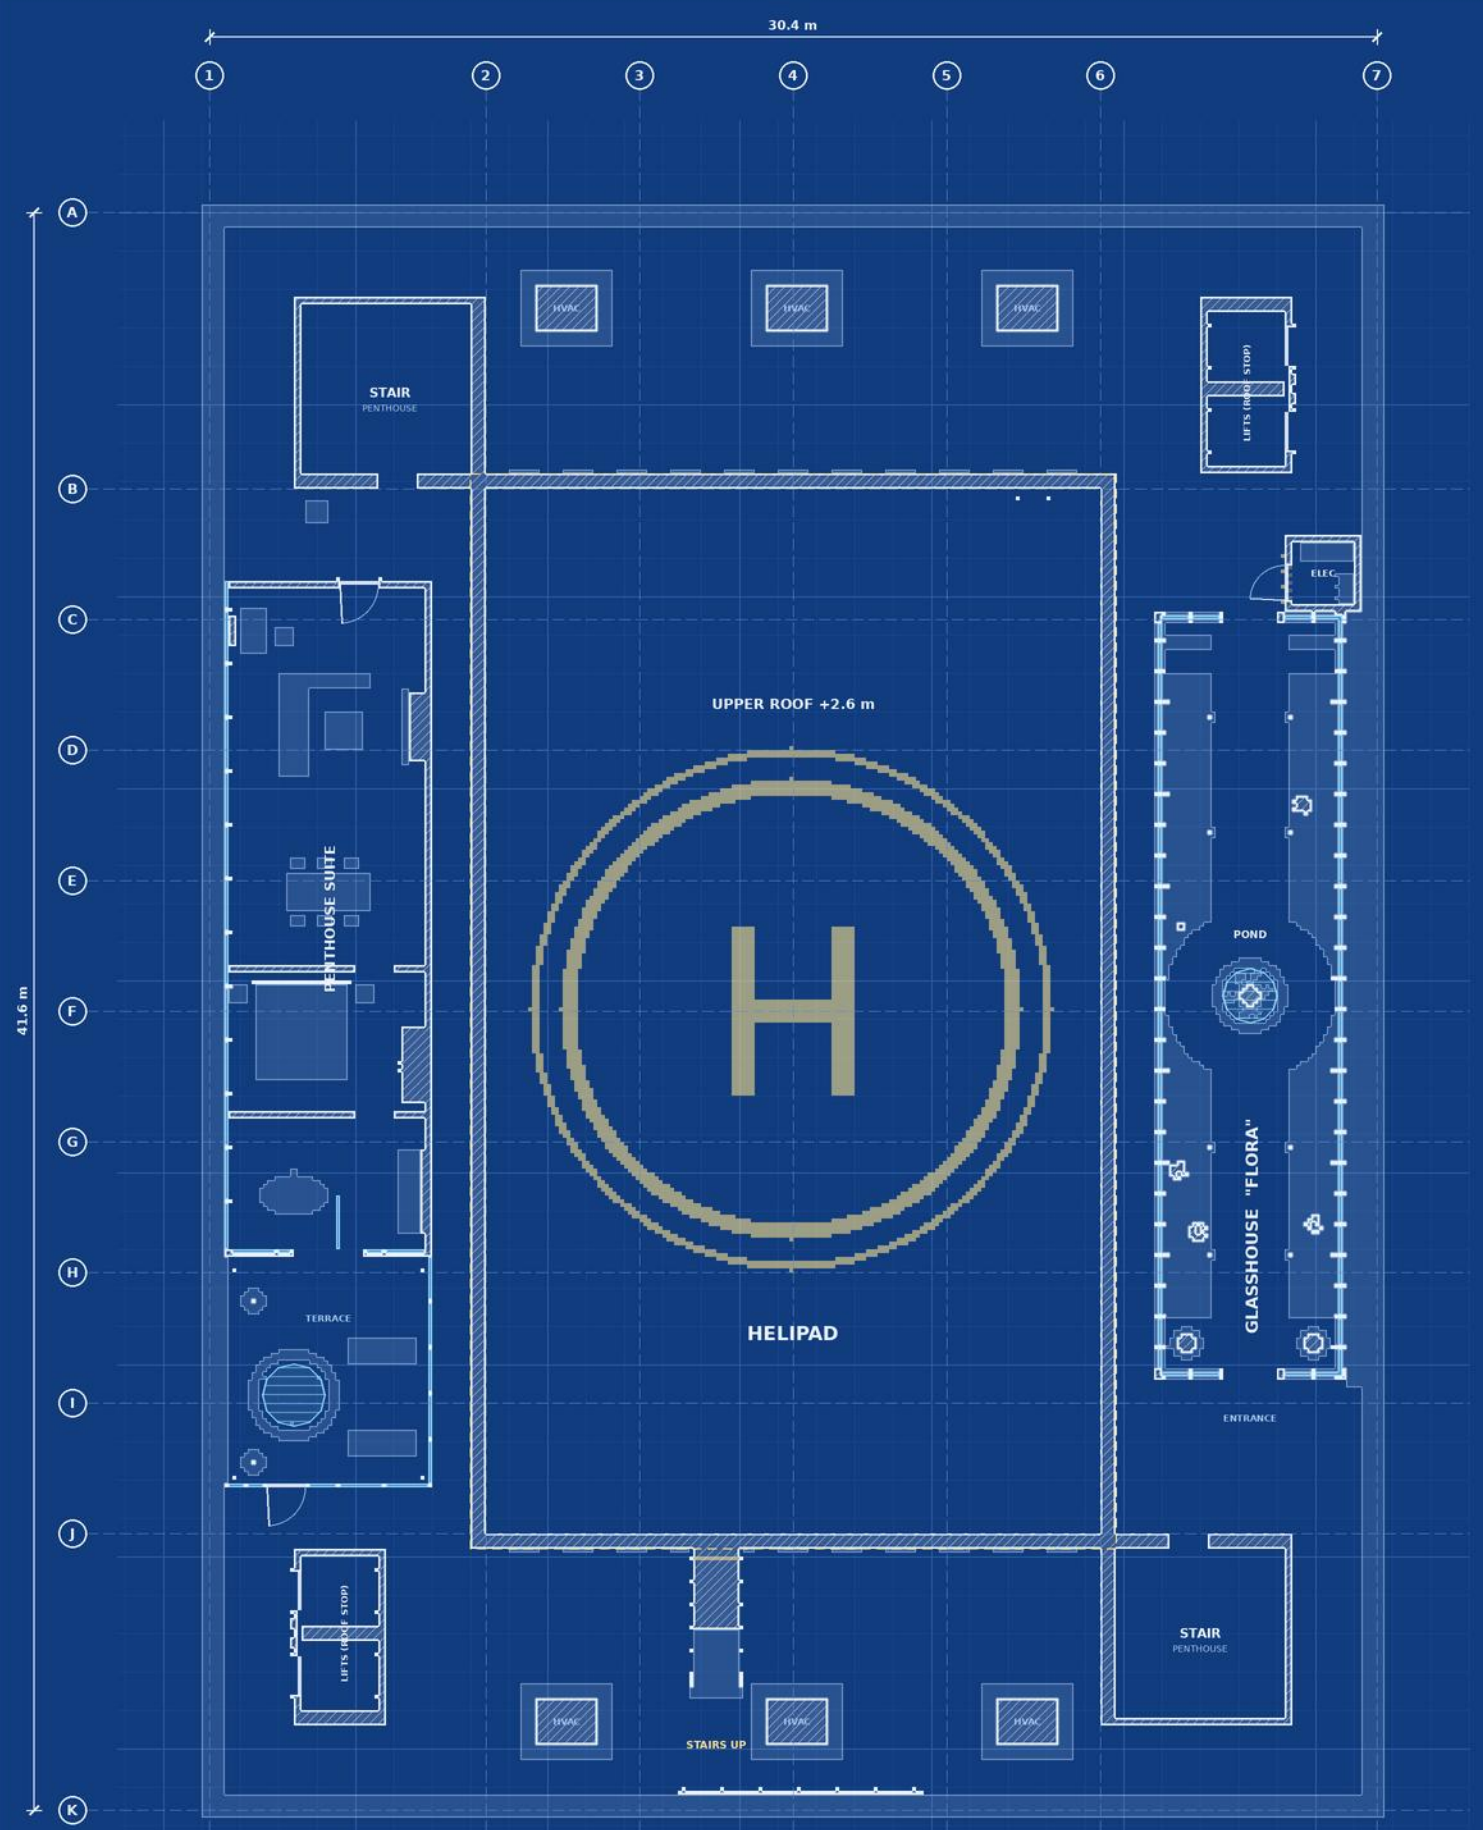

LIMINAL ATRIUM HOTEL

ROOF PLAN - GLASSHOUSE & HELIPAD

Roof +18.0 m, upper roof / helipad +20.6 m. Cut at +1.2 m above the roof.

Glasshouse: glass barrel vault with lantern cupola (not shown), lily pond, palms, beds.
Penthouse: all glass is smart glass (privacy switch by the entrance). ELEC: roof switchgear.
Yellow: helipad markings on the upper roof (dashed outline = upper roof edge).

N

SCALE 1:100 (1 voxel = 10 cm)

0 2.5 5 7.5 10 m

SHEET

A-107

DATE 2026-11-14

DRAWN Claude | SOURCE tools/build_map.py

Teardown map mod - Liminal Atrium