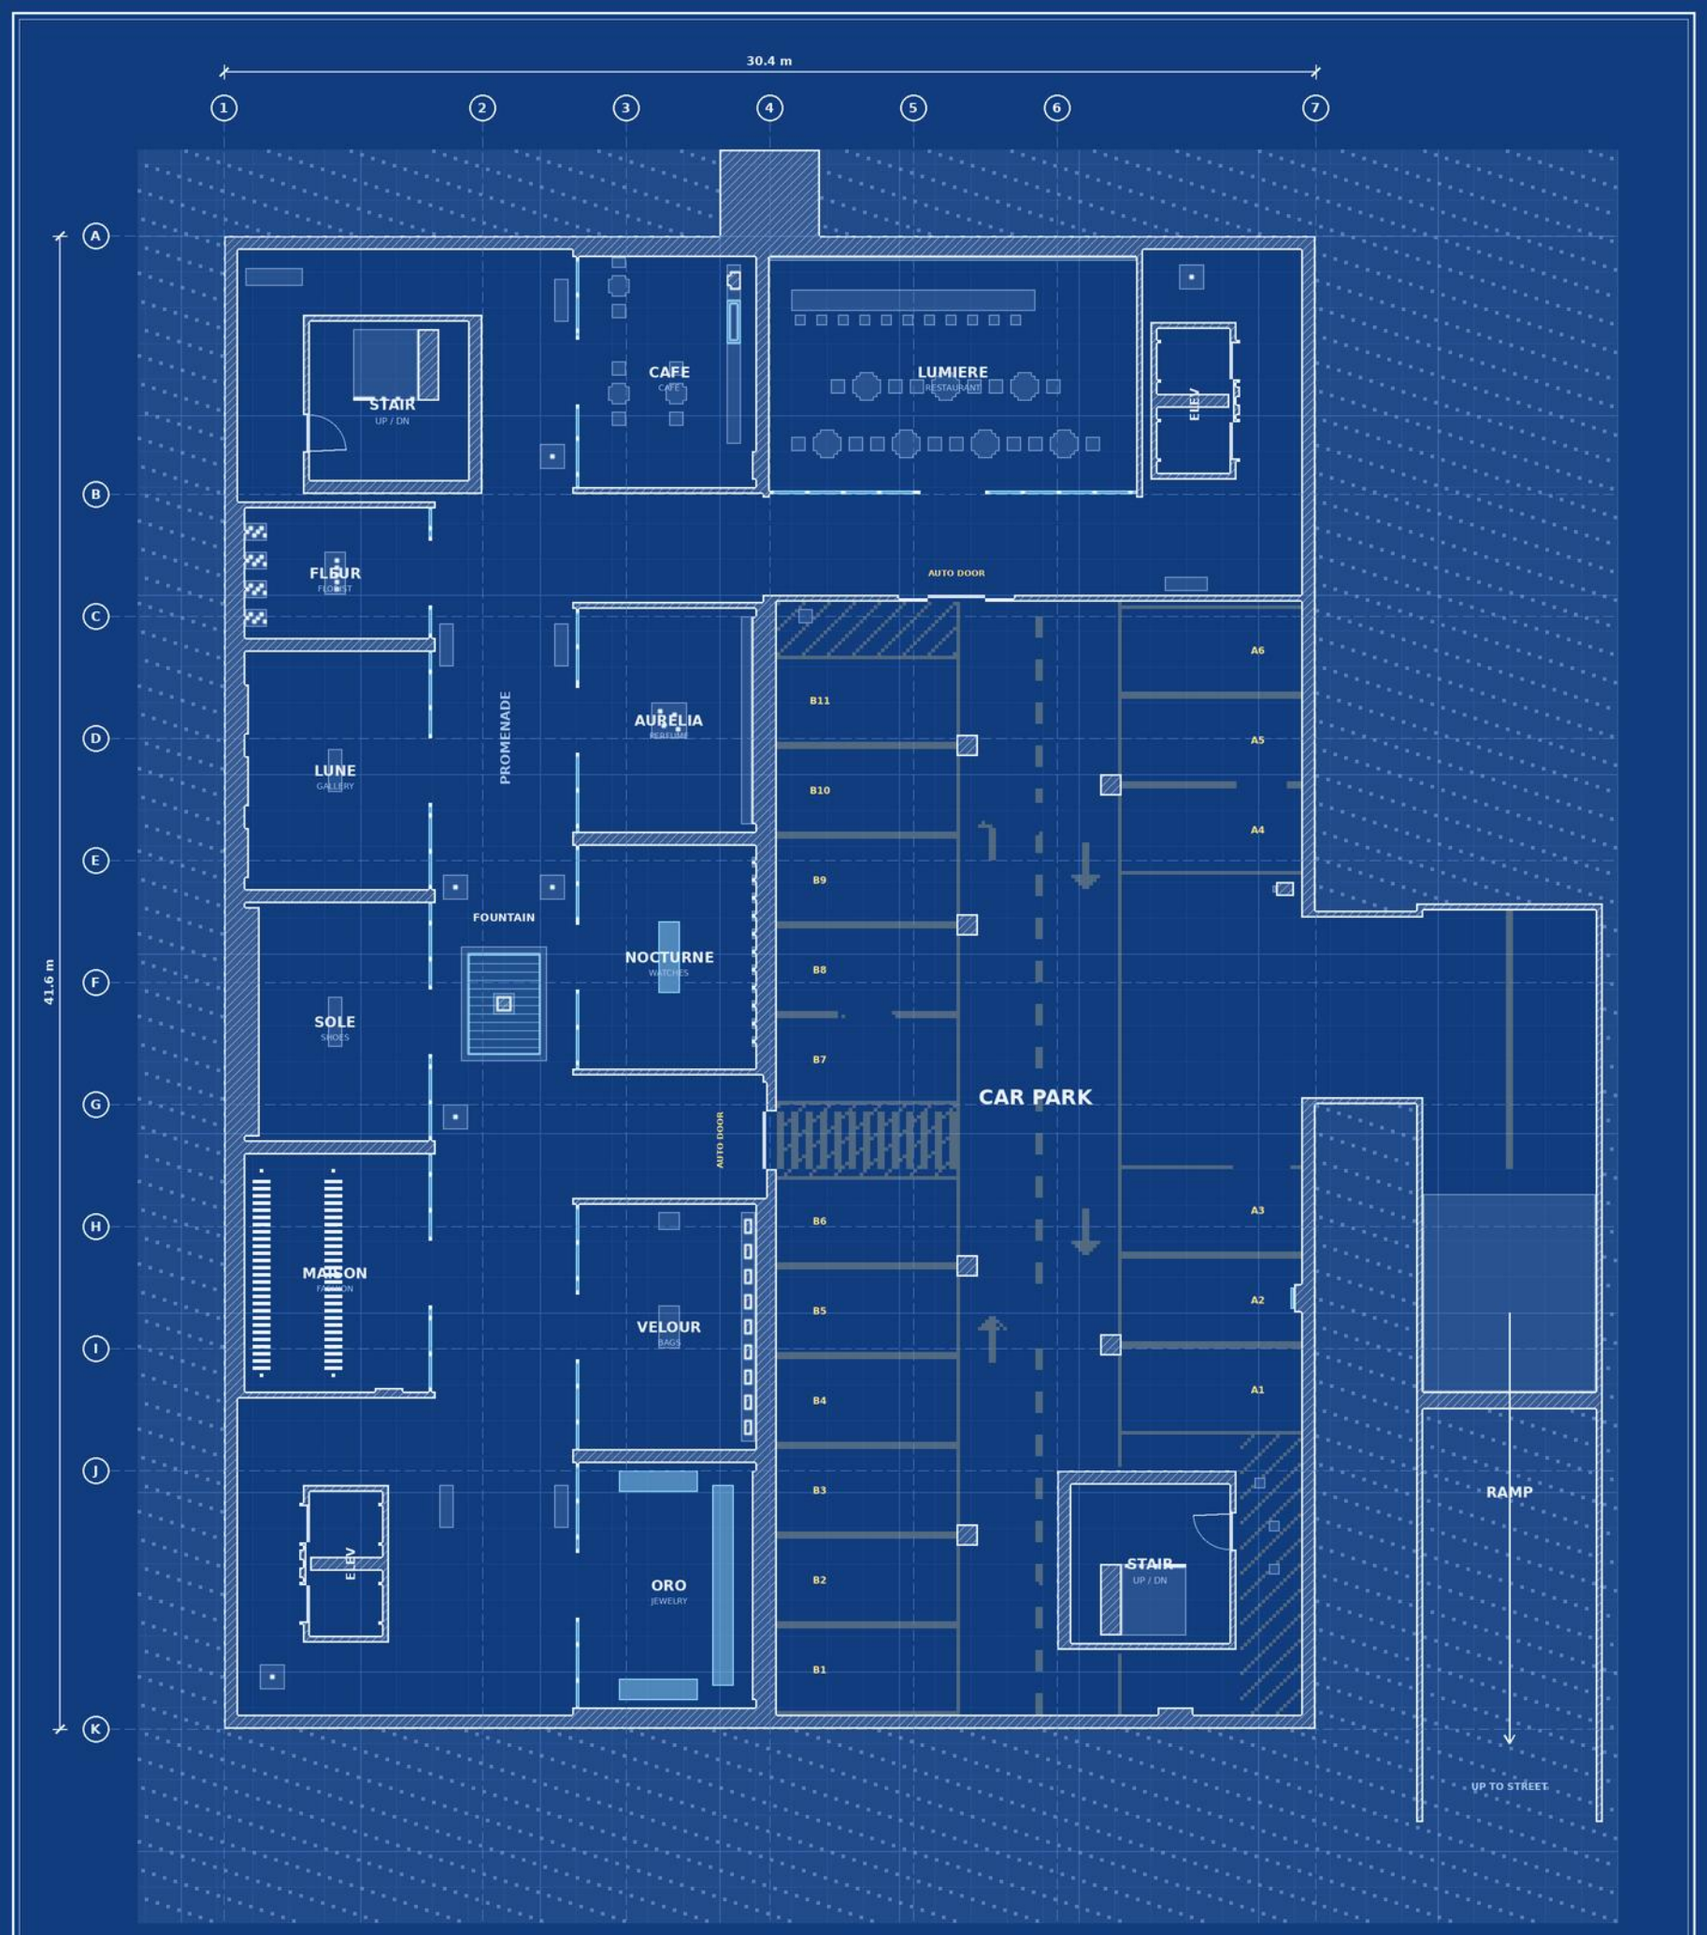


LIMINAL ATRIUM HOTEL

LEVEL B1 - CAR PARK & LUXURY ARCADE

Floor -3.6 m. Cut at +1.2 m above floor.

Parking: 17 bays 2.5 x 5.0 m (A1-A6, B1-B11), 90-degree, reverse in.
Columns 0.6 x 0.6 m on the aisle edge. Hatched: no parking.

N

SCALE 1:100 (1 voxel = 10 cm)

0 2.5 5 7.5 10 m

SHEET

A-100

DATE 2026-11-14

DRAWN Claude | SOURCE tools/build_map.py

Teardown map mod - Liminal Atrium

LIMINAL ATRIUM HOTEL

LEVEL 1 - LOBBY, GUEST ROOMS & POOLROOMS

Floor +/-0.0 (pool hall deck +2.0 m). Cut at +1.2 m above floor.

Room numbers are drawing references (floor x 100 + room).
Pool hall deck is 2.0 m above the ground floor; shown cut at +1.2 m from the deck.


SCALE 1:100 (1 voxel = 10 cm)

0 2.5 5 7.5 10 m

N

SHEET
A-101

DATE 2026-11-14
DRAWN Claude | SOURCE tools/build_map.py
Teardown map mod - Liminal Atrium

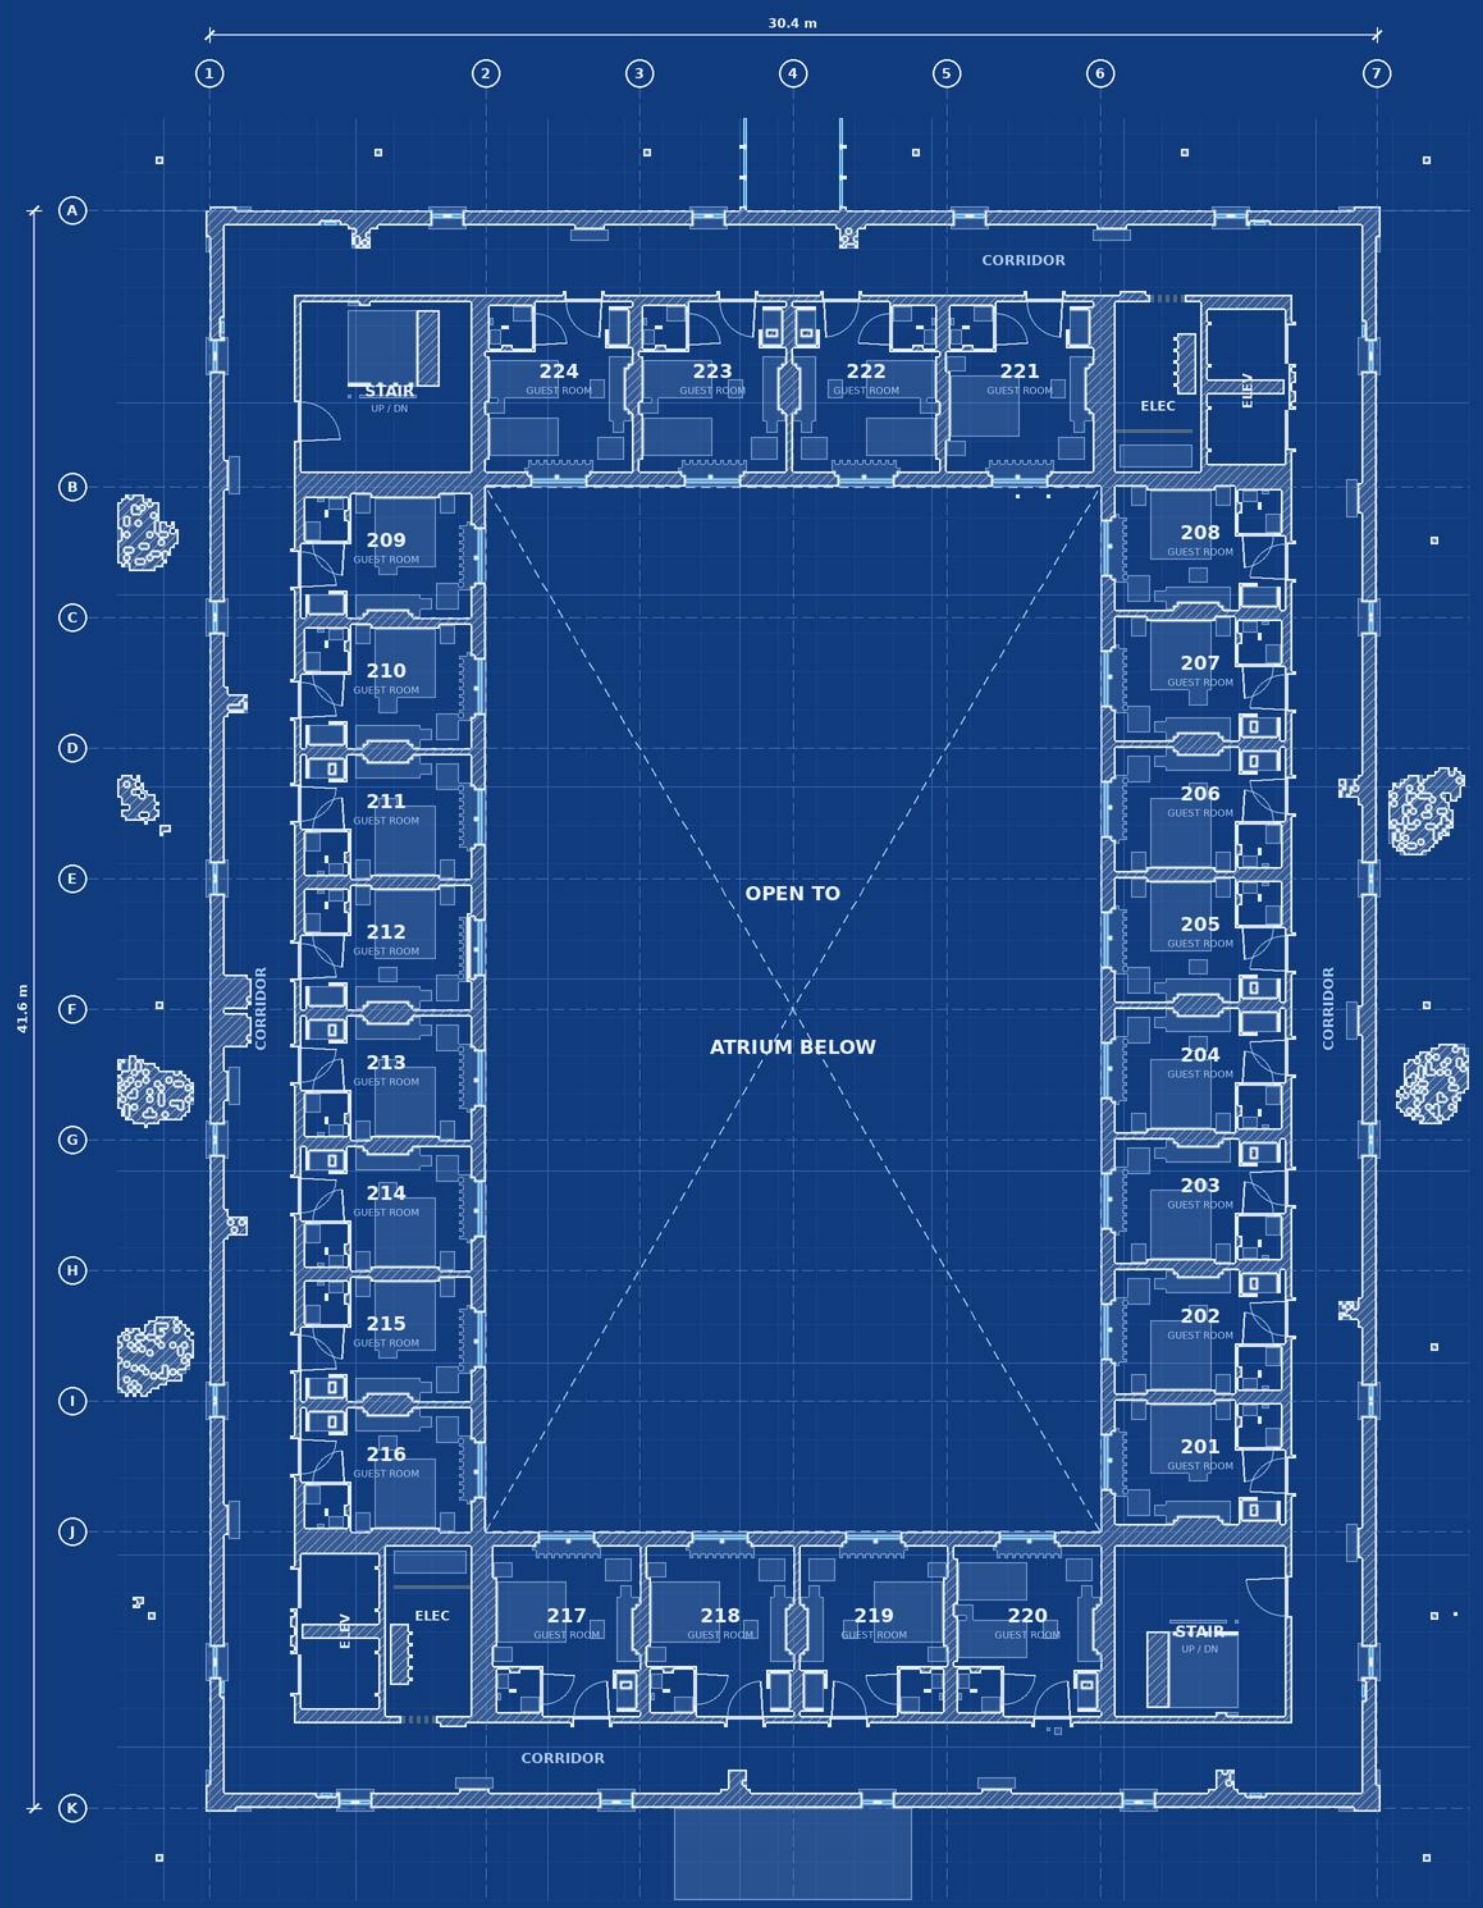

LIMINAL ATRIUM HOTEL

LEVEL 2 - GUEST FLOOR

Floor +3.0 m. Cut at +1.2 m above floor. Corridor theme: zigzag.

Room numbers are drawing references (floor x 100 + room).
Electrical rooms by the elevators feed this floor (E: switch, destroyed: blackout).

N

SCALE 1:100 (1 voxel = 10 cm)

0 2.5 5 7.5 10 m


SHEET

A-102

DATE 2026-11-14

DRAWN Claude | SOURCE tools/build_map.py

Teardown map mod - Liminal Atrium

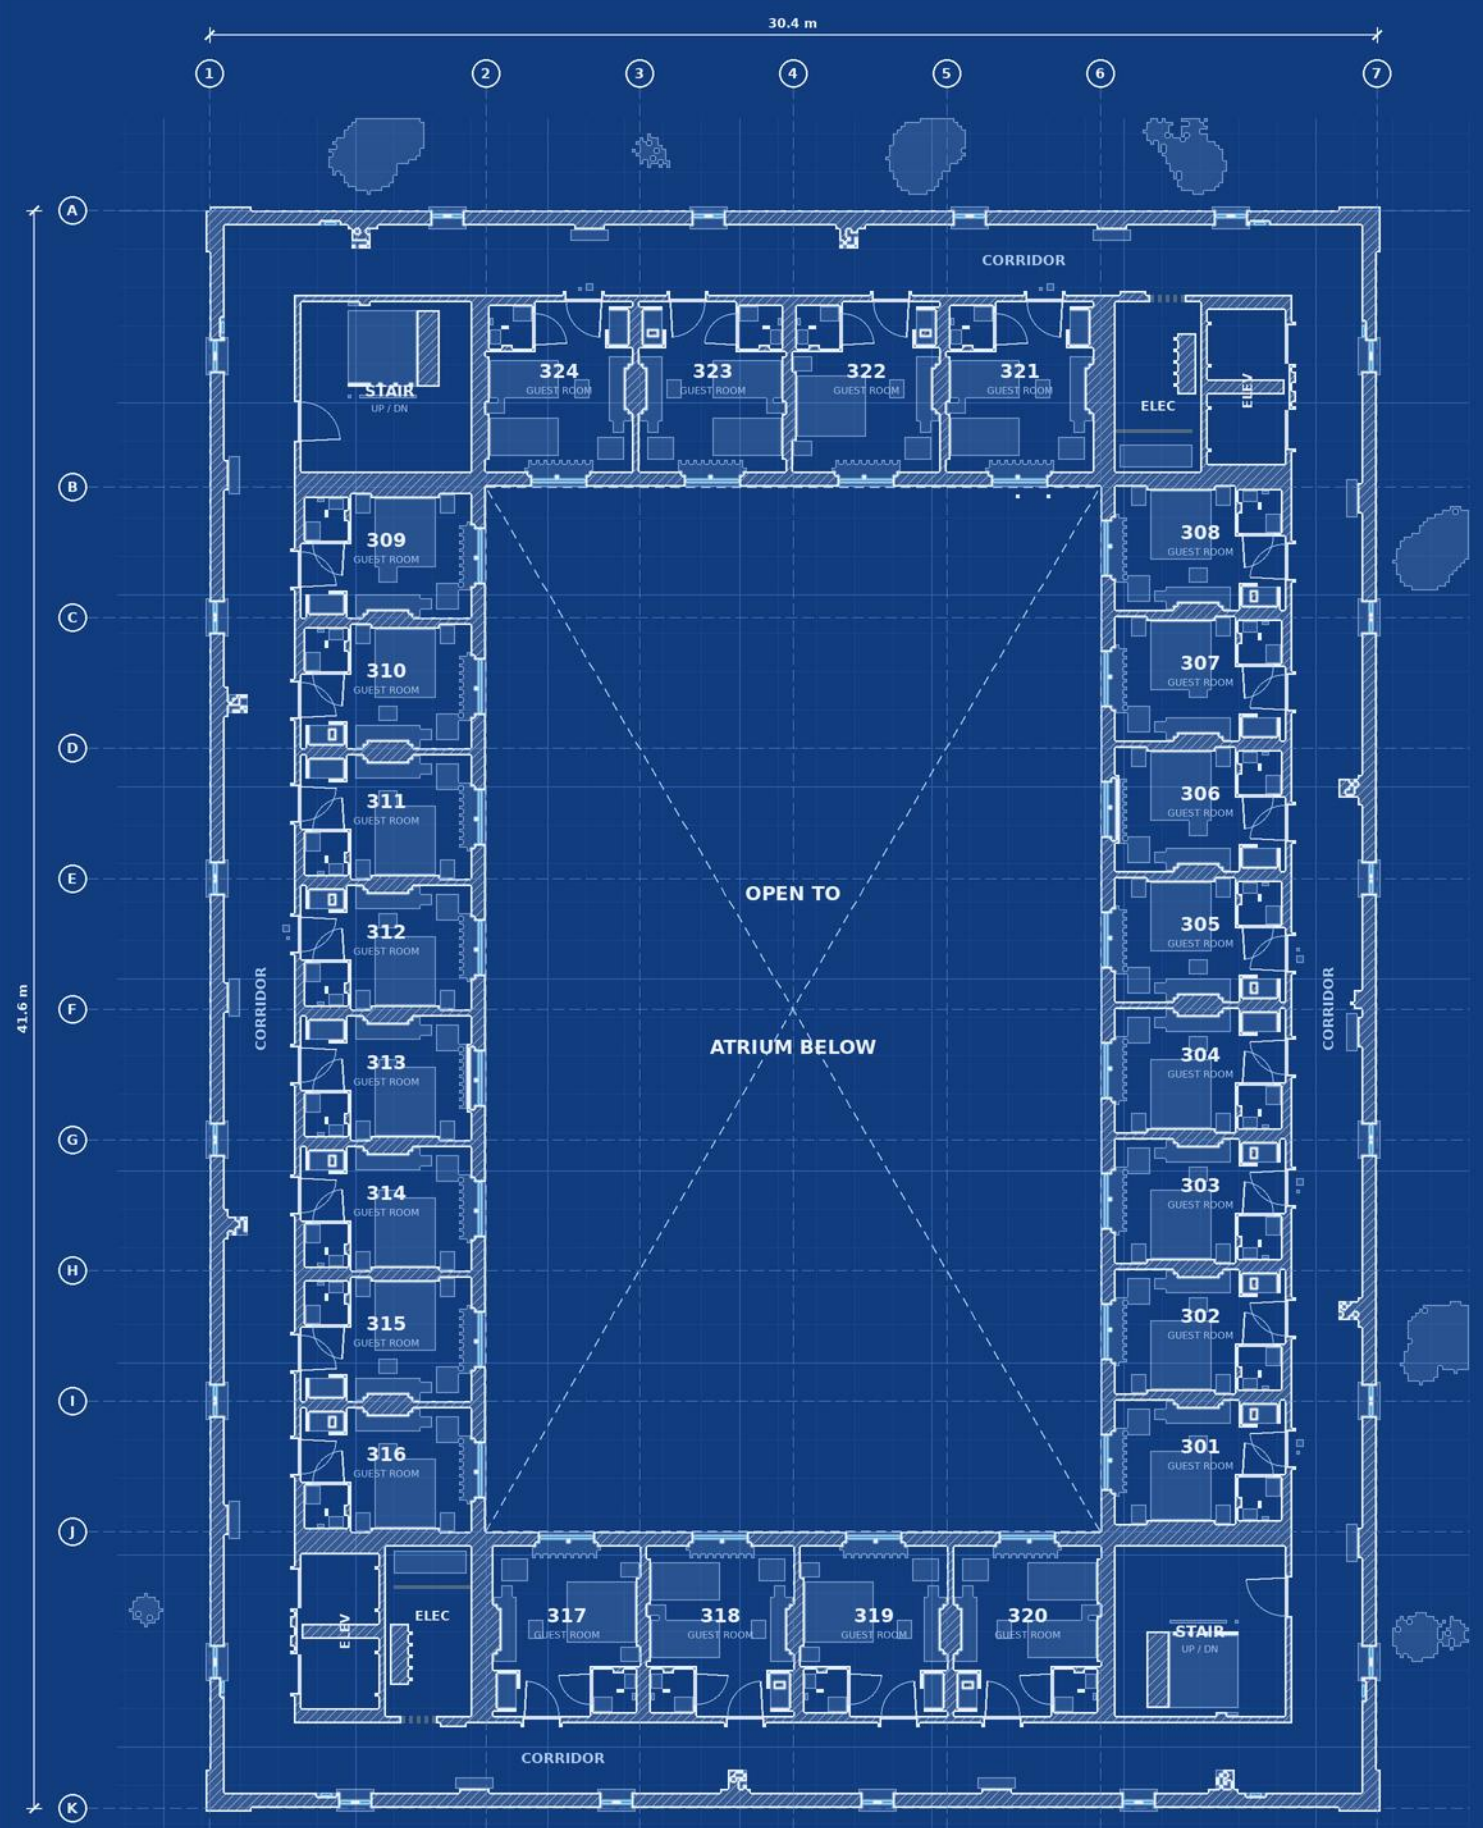

LIMINAL ATRIUM HOTEL

LEVEL 3 - GUEST FLOOR

Floor +6.0 m. Cut at +1.2 m above floor. Corridor theme: diamond.

Room numbers are drawing references (floor x 100 + room).
Electrical rooms by the elevators feed this floor (E: switch, destroyed: blackout).

N

SCALE 1:100 (1 voxel = 10 cm)

0 2.5 5 7.5 10 m


SHEET

A-103

DATE 2026-11-14

DRAWN Claude | SOURCE tools/build_map.py

Teardown map mod - Liminal Atrium

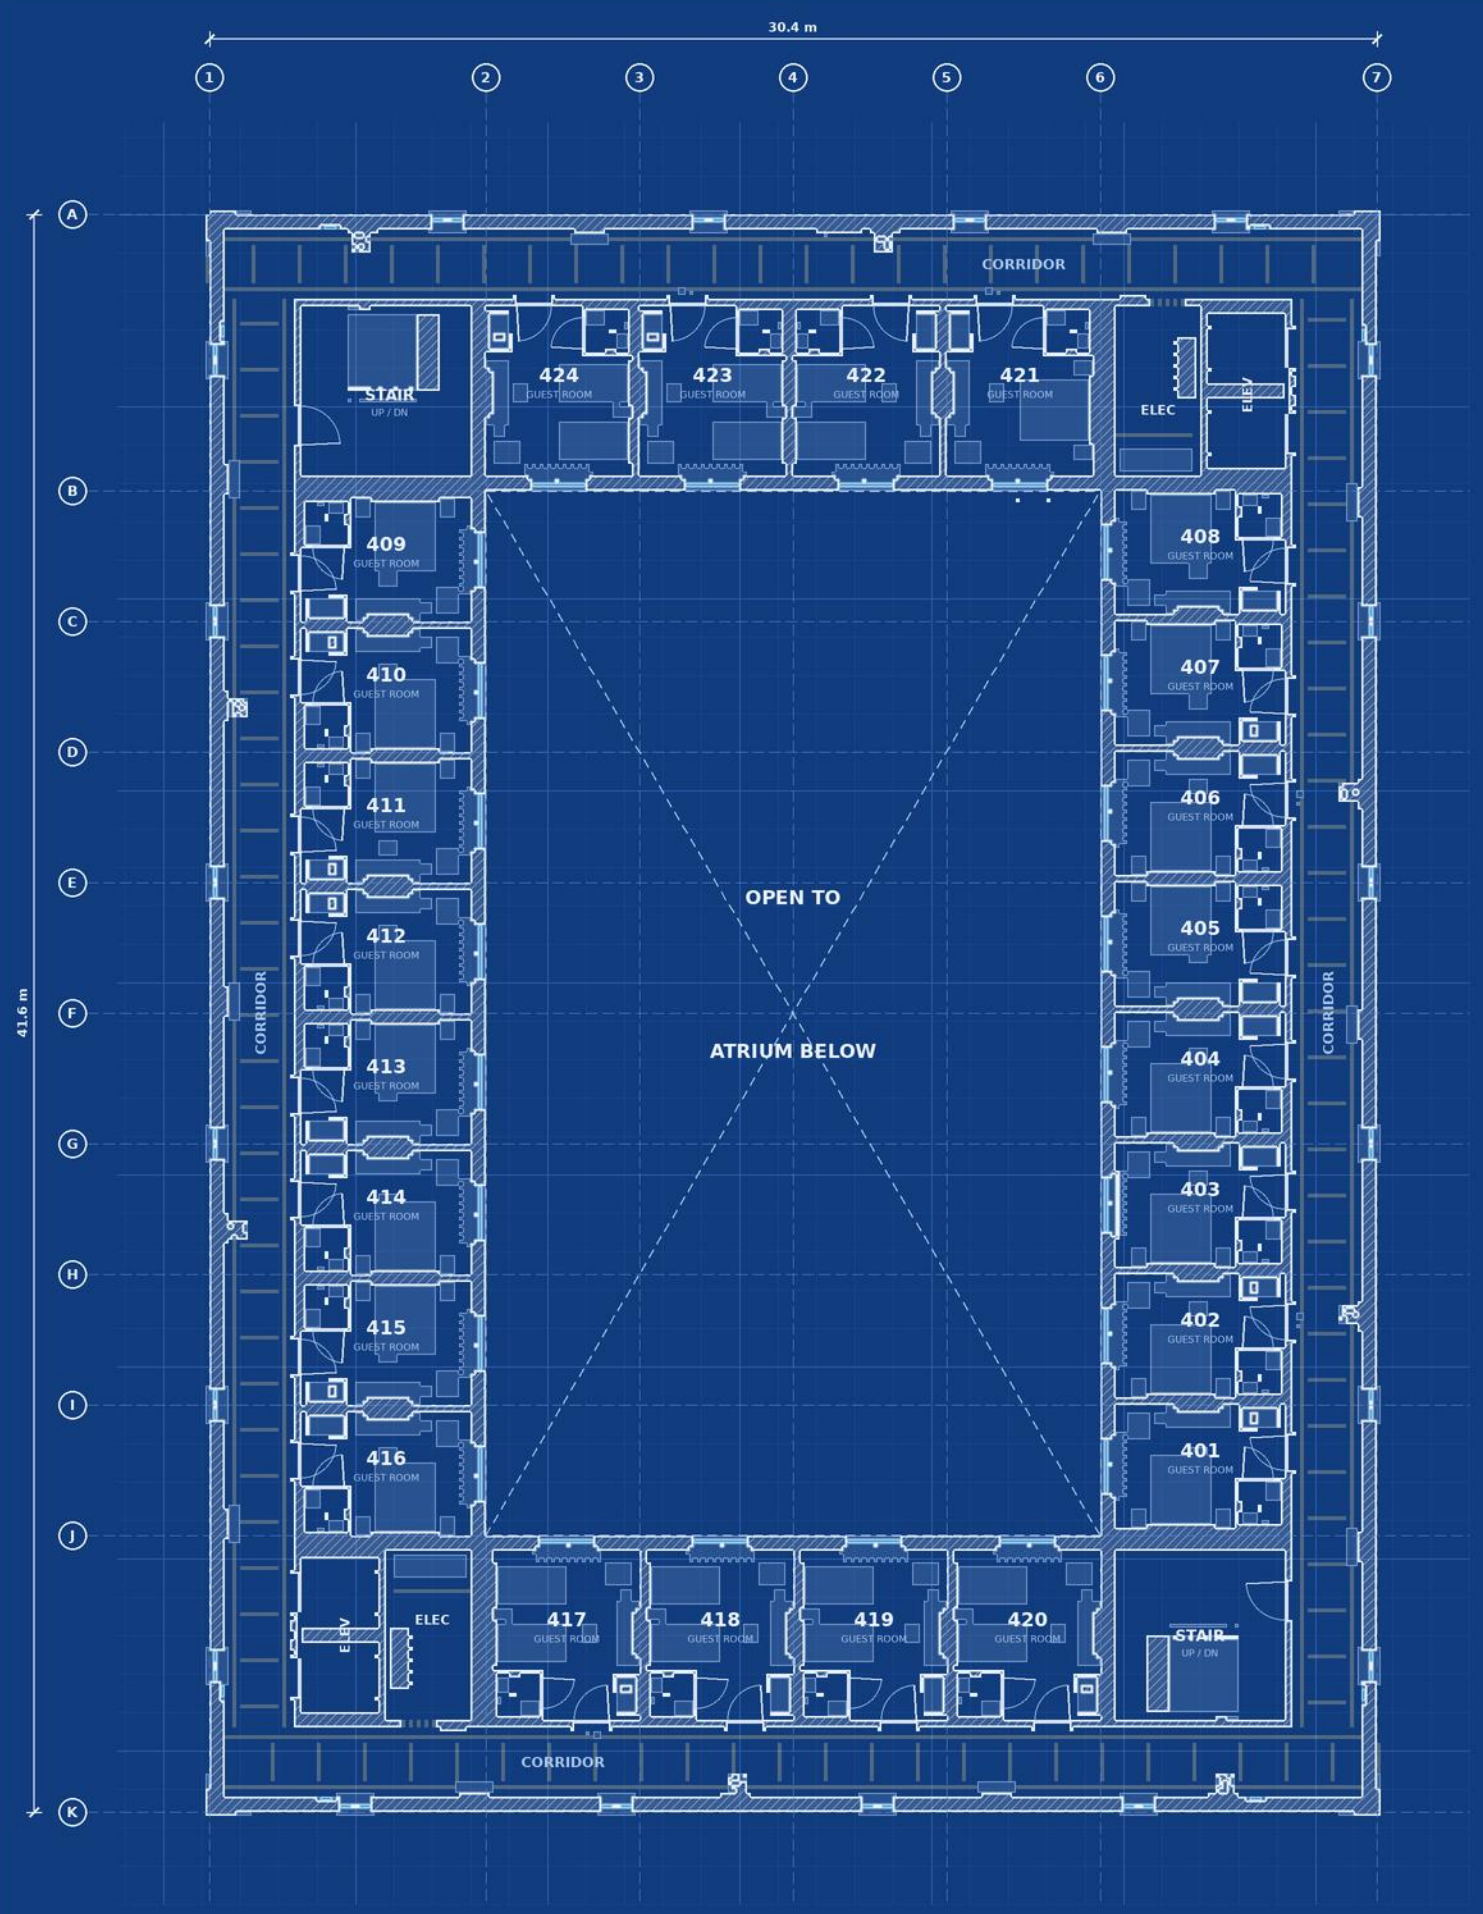

LIMINAL ATRIUM HOTEL

LEVEL 4 - GUEST FLOOR

Floor +9.0 m. Cut at +1.2 m above floor. Corridor theme: stripes.

Room numbers are drawing references (floor x 100 + room).
Electrical rooms by the elevators feed this floor (E: switch, destroyed: blackout).

N

SCALE 1:100 (1 voxel = 10 cm)

0 2.5 5 7.5 10 m


SHEET

A-104

DATE 2026-11-14

DRAWN Claude | SOURCE tools/build_map.py

Teardown map mod - Liminal Atrium

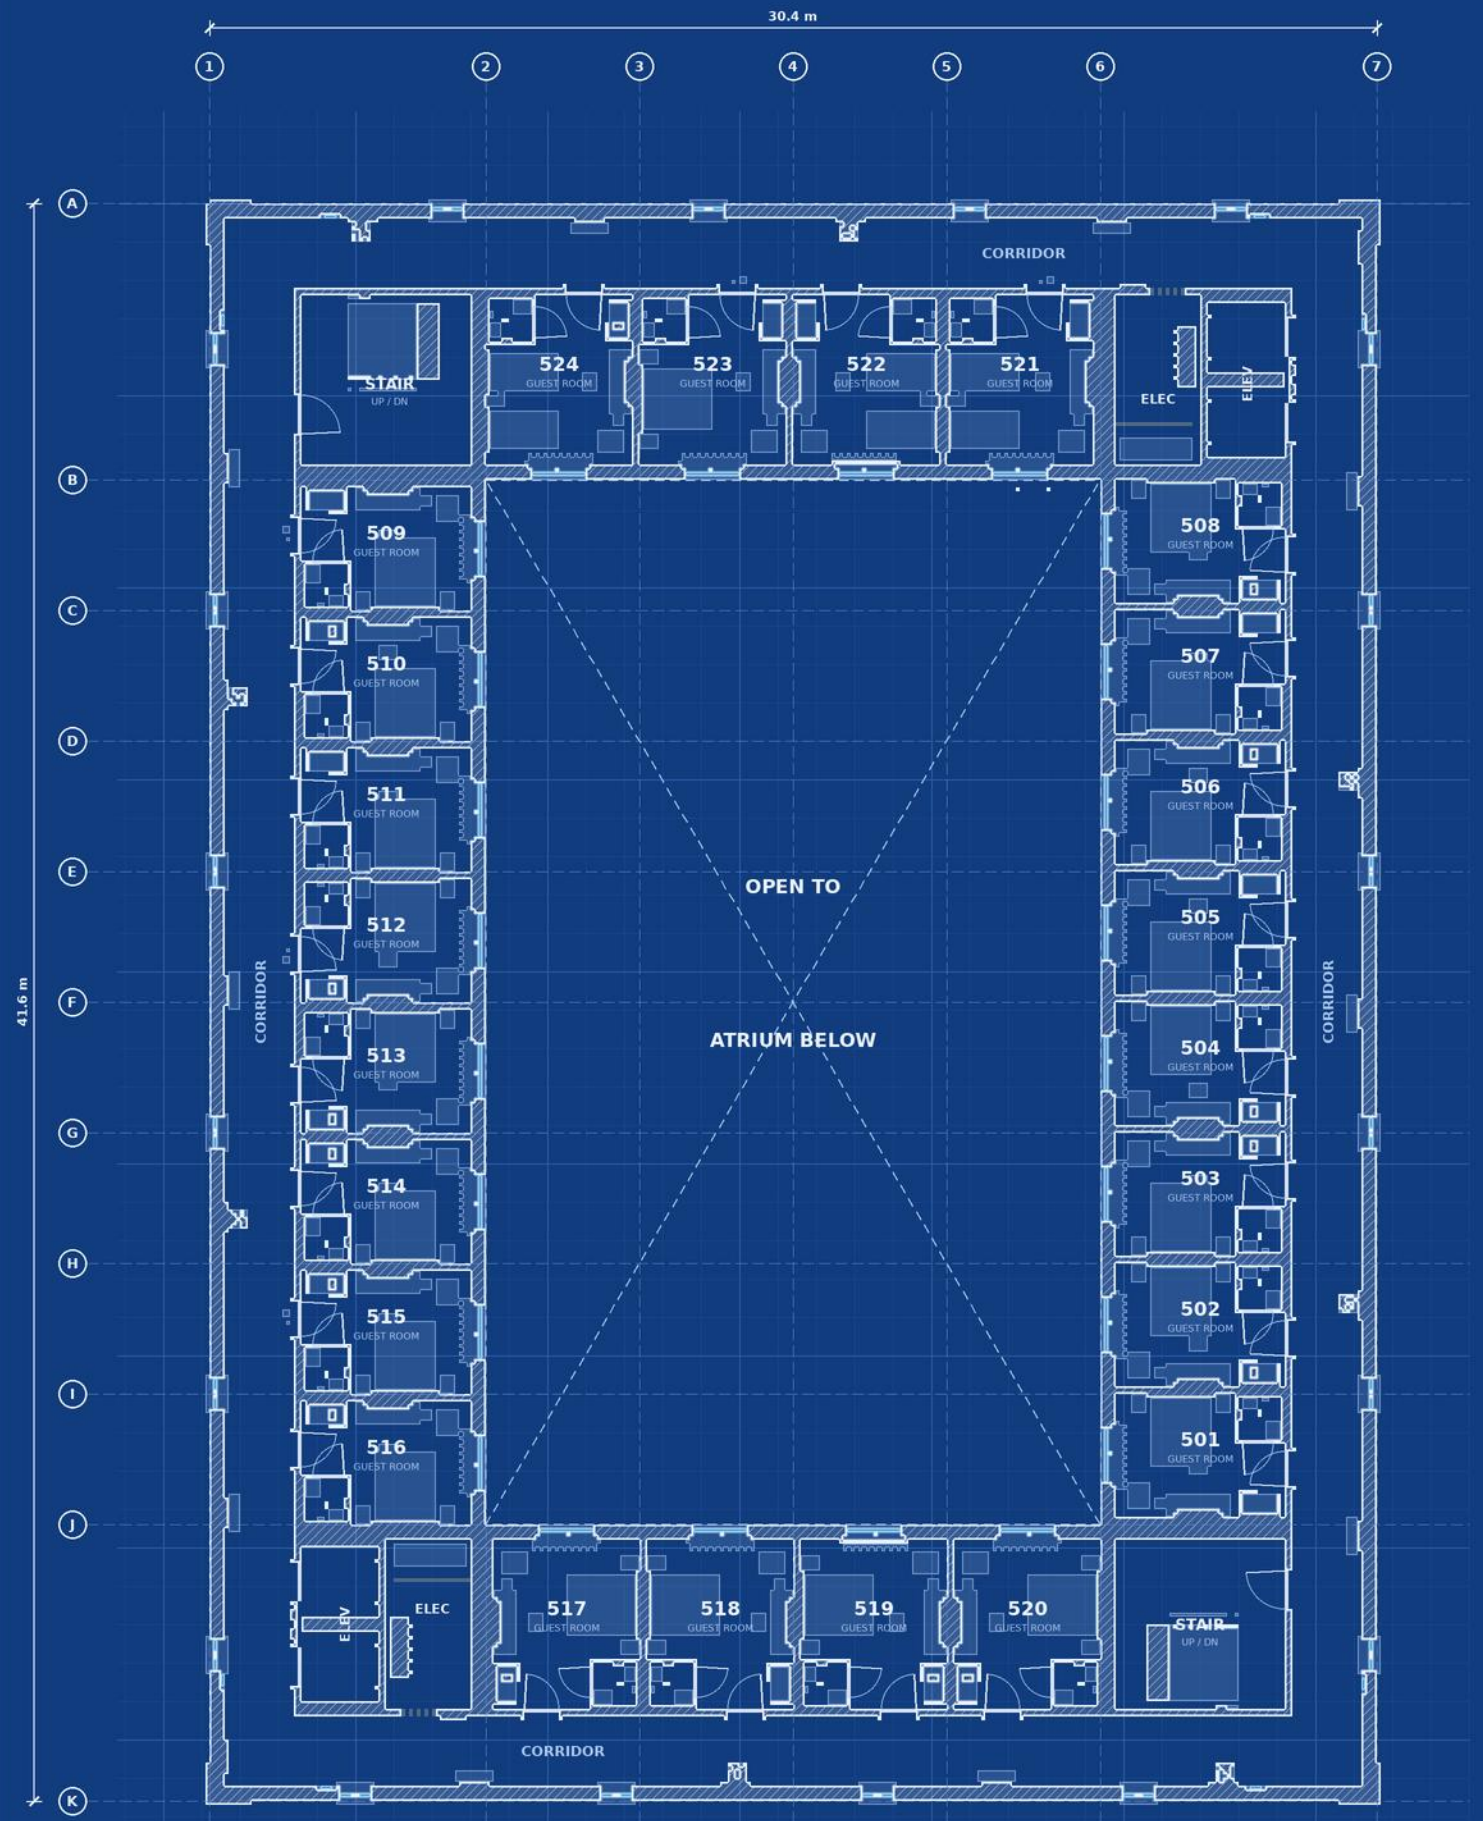

LIMINAL ATRIUM HOTEL

LEVEL 5 - GUEST FLOOR

Floor +12.0 m. Cut at +1.2 m above floor. Corridor theme: dots.

Room numbers are drawing references (floor x 100 + room).
Electrical rooms by the elevators feed this floor (E: switch, destroyed: blackout).

N

SCALE 1:100 (1 voxel = 10 cm)

0 2.5 5 7.5 10 m


SHEET

A-105

DATE 2026-11-14

DRAWN Claude | SOURCE tools/build_map.py

Teardown map mod - Liminal Atrium

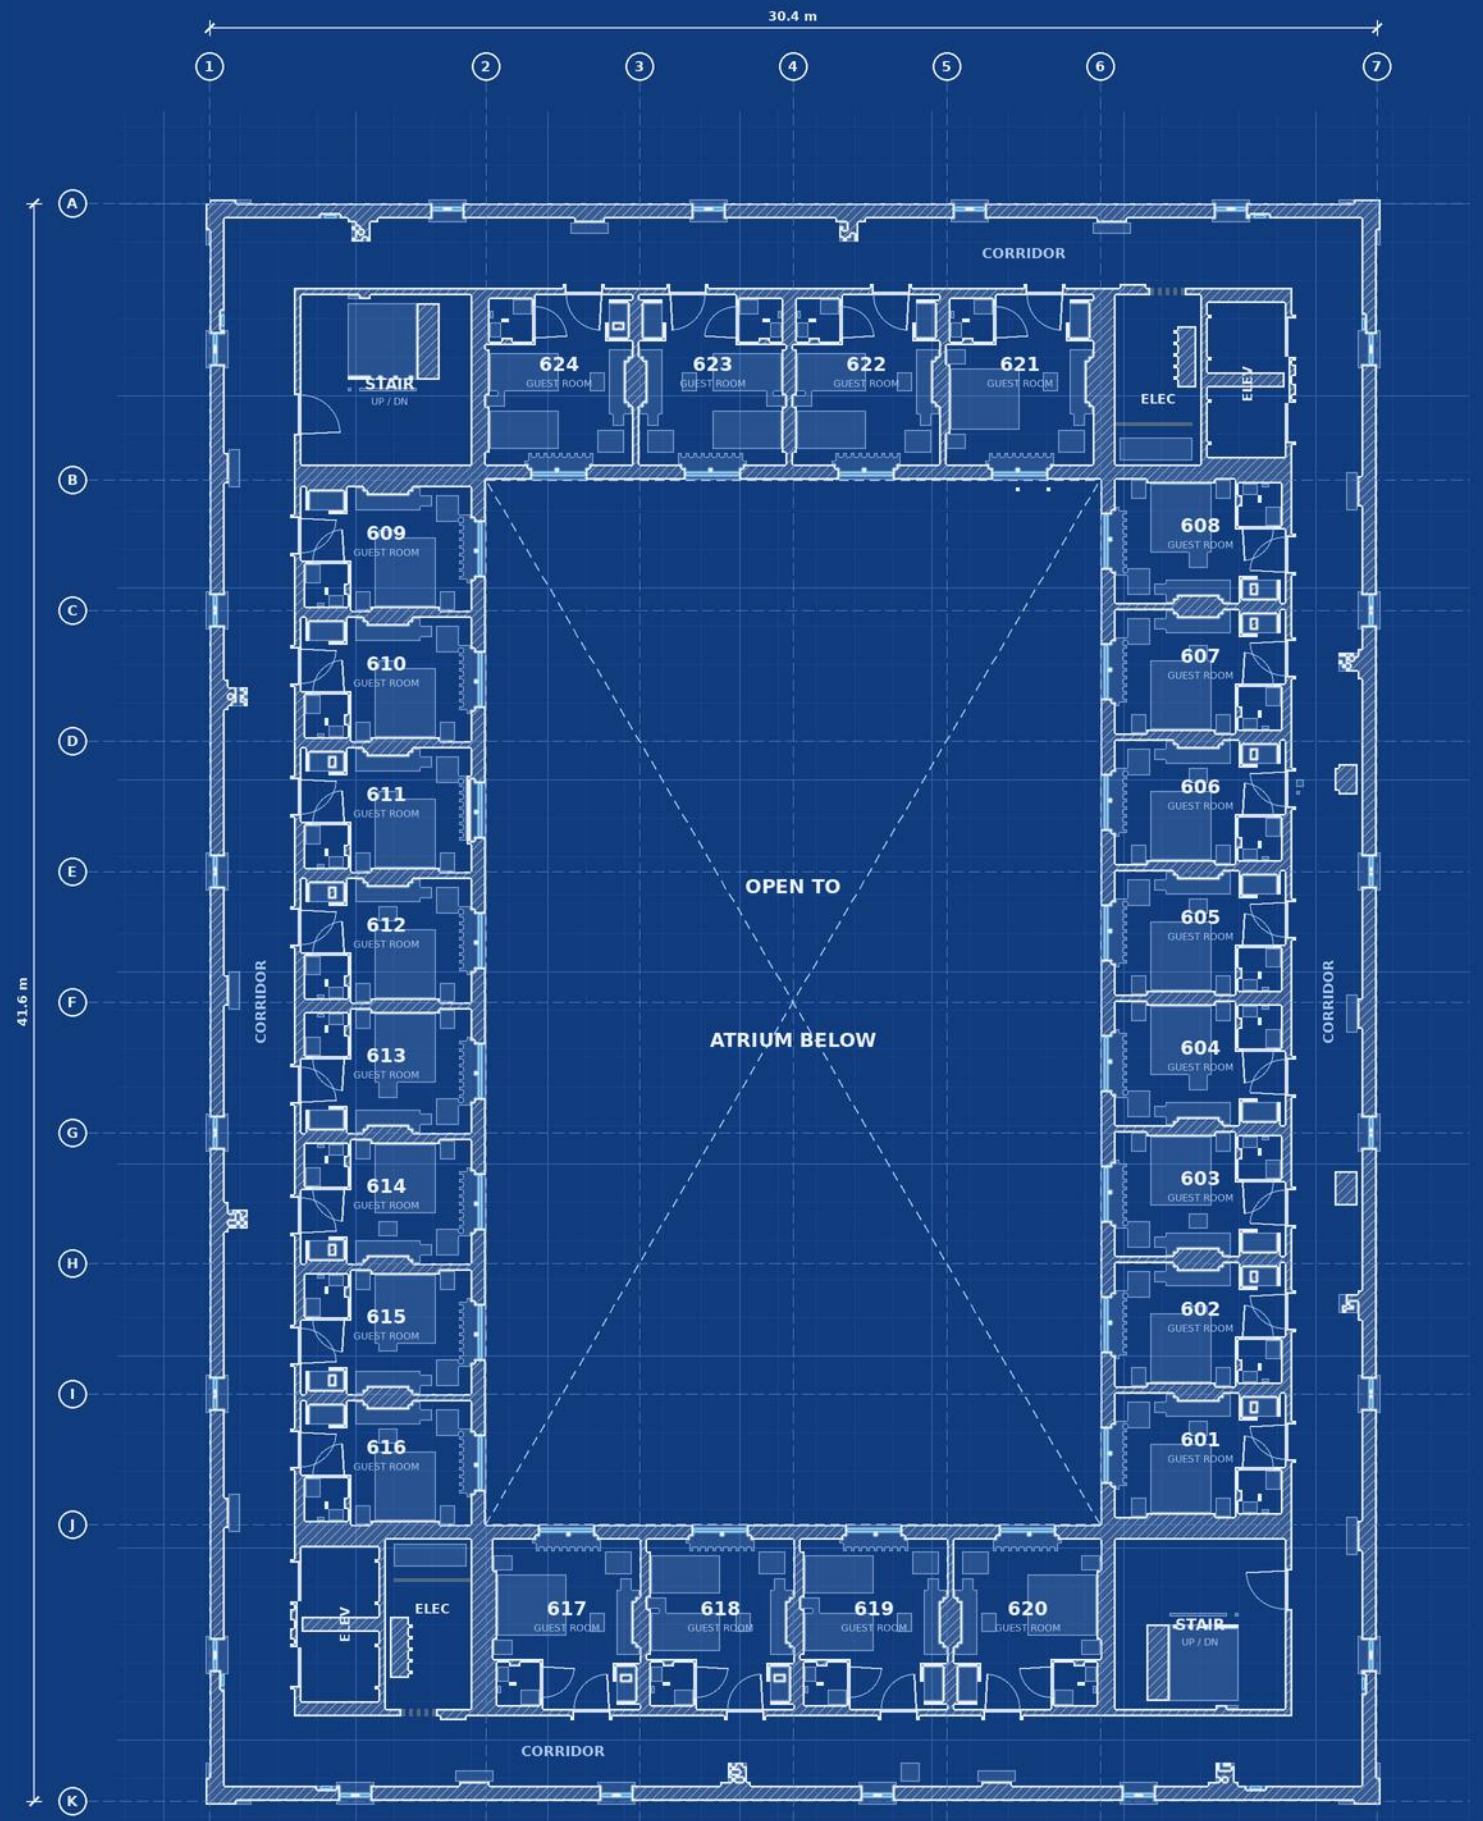

LIMINAL ATRIUM HOTEL

LEVEL 6 - GUEST FLOOR

Floor +15.0 m. Cut at +1.2 m above floor. Corridor theme: plain.

Room numbers are drawing references (floor x 100 + room).
Electrical rooms by the elevators feed this floor (E: switch, destroyed: blackout).

N

SCALE 1:100 (1 voxel = 10 cm)

0 2.5 5 7.5 10 m


SHEET

A-106

DATE 2026-11-14

DRAWN Claude | SOURCE tools/build_map.py

Teardown map mod - Liminal Atrium

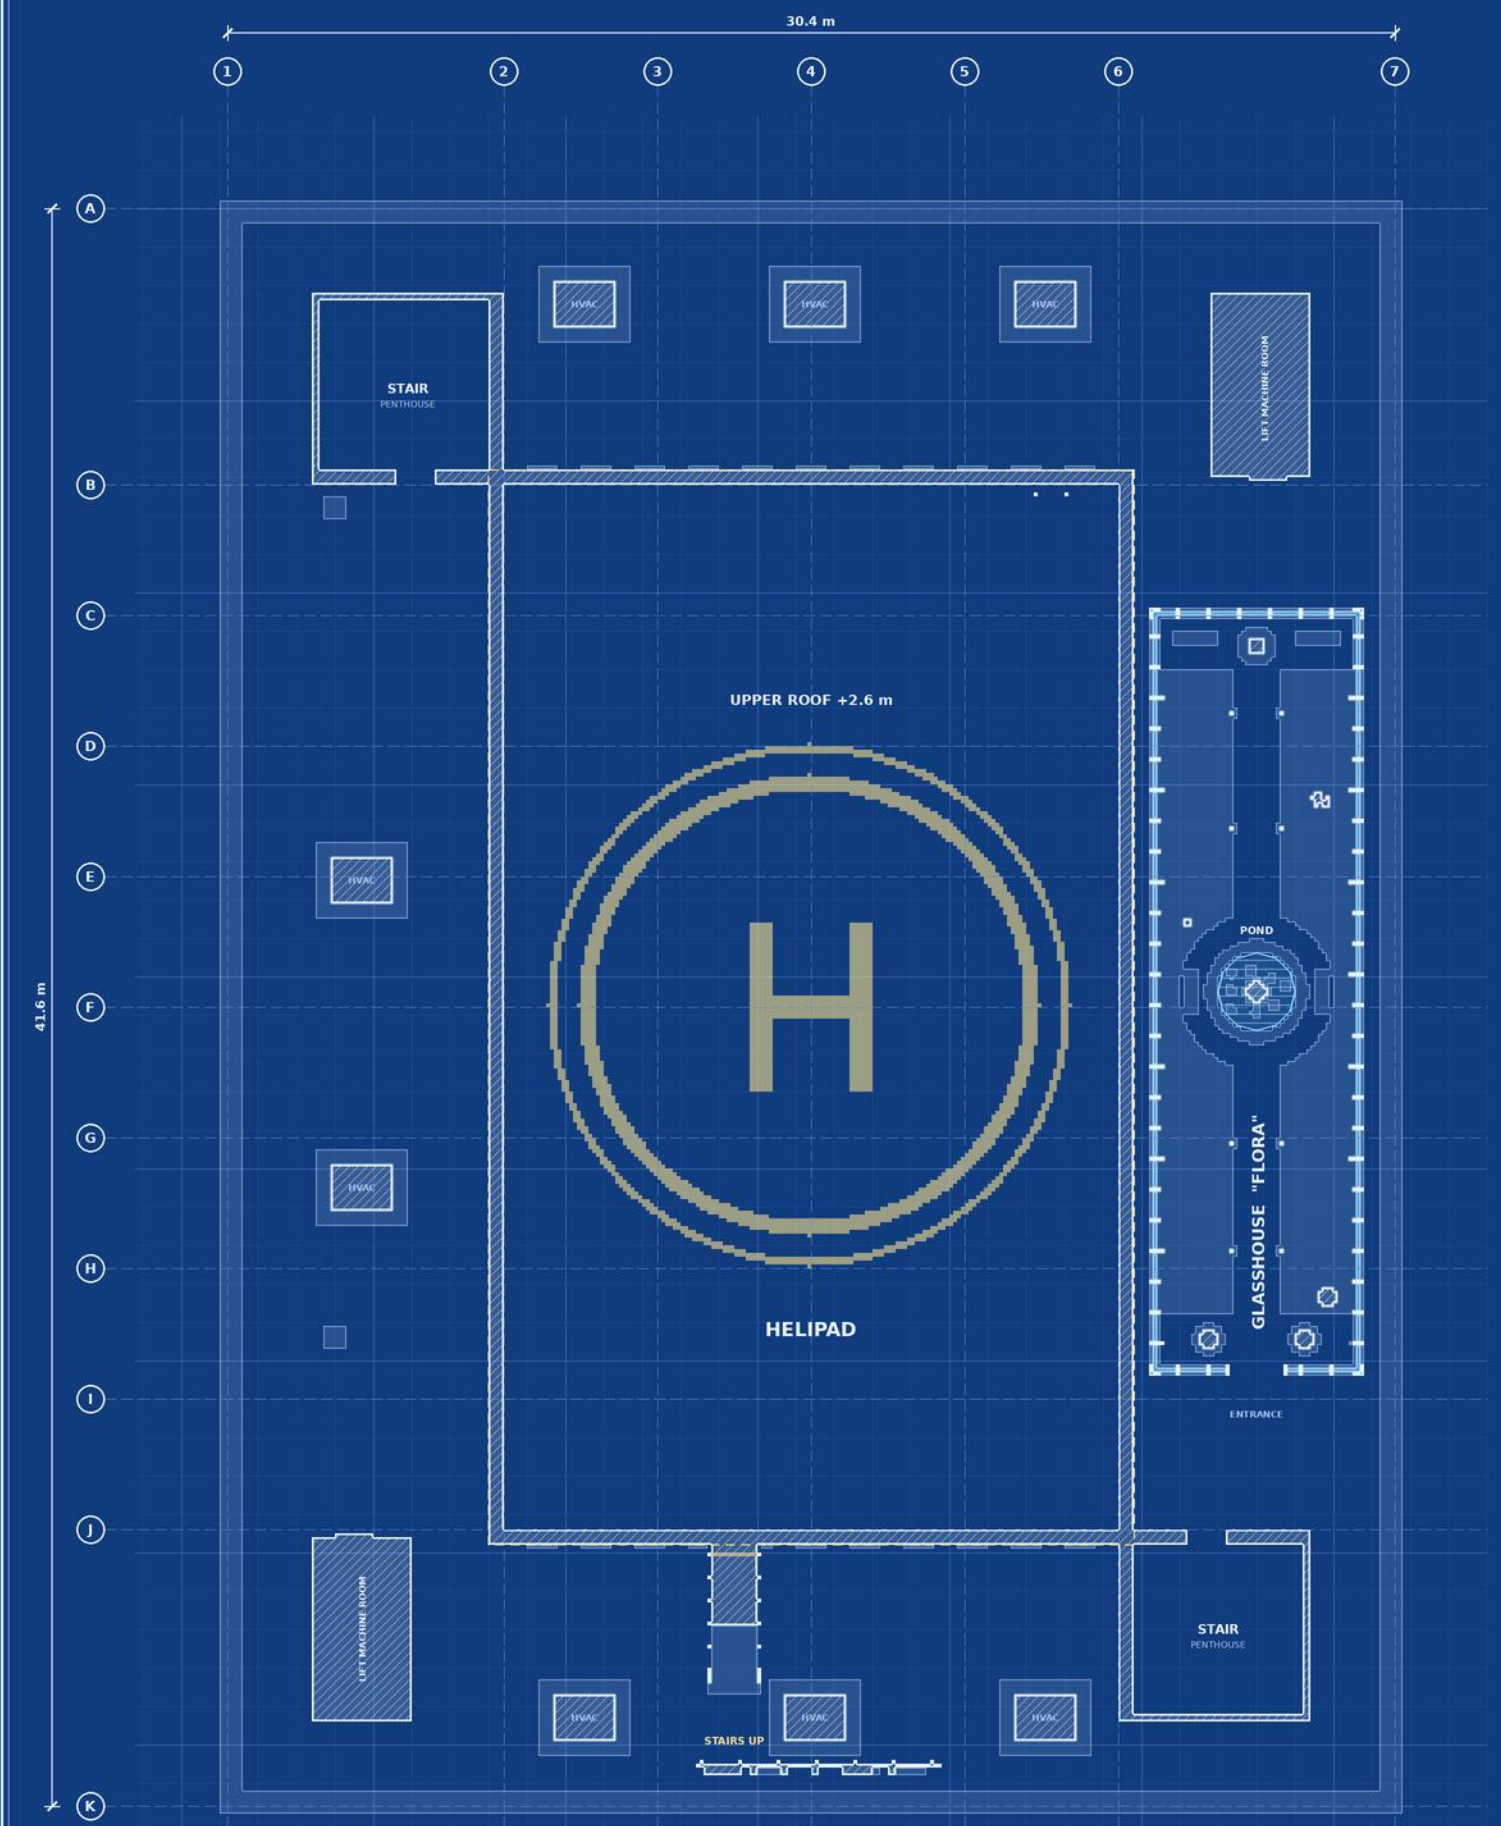

LIMINAL ATRIUM HOTEL

ROOF PLAN - GLASSHOUSE & HELIPAD

Roof +18.0 m, upper roof / helipad +20.6 m. Cut at +1.2 m above the roof.

Glasshouse: glass barrel vault with lantern cupola (not shown), lily pond, palms, beds.
Yellow: helipad markings on the upper roof (dashed outline = upper roof edge).

N

SCALE 1:100 (1 voxel = 10 cm)

0 2.5 5 7.5 10 m

SHEET

A-107

DATE 2026-11-14

DRAWN Claude | SOURCE tools/build_map.py

Teardown map mod - Liminal Atrium